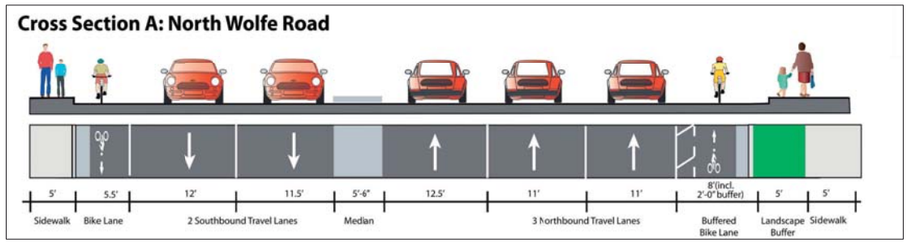

General Notes

1. Do not scale drawings. Dimensions govern.
2. All dimensions are in feet and inches unless noted otherwise.
3. All dimensions shall be verified on site before proceeding with the work.
4. Foster + Partners shall be notified in writing of any discrepancies.
5. Any areas indicated on this sheet are approximate and indicative only.

Rev.	Date	Reason For Issue	Chk
00	04/12/13	Planning Revision 06	

Key Plan

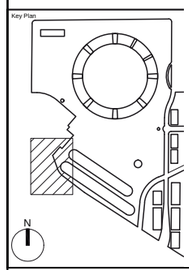

Foster + Partners
Riverside, 22 Hester Road
London SW11 4AN
T +44 (0)20 7738 0455
F +44 (0)20 7738 1107

© Foster + Partners 2010

ARUP
Arup North America Ltd.
560 Mission Street, Suite 700
San Francisco, CA 94105, USA
Tel (415) 926 0200 Fax (415) 957 9096
www.arup.com

OLIN
LANDSCAPE ARCHITECTURE AND URBAN DESIGN
PUBLIC LEDGER BUILDING,SUITE 1123
150 SOUTH INDEPENDENCE MALL WEST
PHILADELPHIA, PA 19106
TEL 215.440.0030 / FAX 215.440.0041
WWW.THEOLINSTUDIO.COM
OLIN PARTNERSHIP, LTD.

KIER & WRIGHT
3350 Scott Boulevard, Building 22
Santa Clara, California 95054
Phone: (408) 727-6665 Fax: (408) 727 5641
www.kierwright.com

© Kier & Wright, 2011

alta
2560 9th Street, Suite 212
Berkeley, CA 94710
p:510.540.5008 f:510.540.5039
www.altaplanning.com

Client
Apple Inc.

Project
Apple Campus 2

Title
Perimeter Bicycle Strategy

Project No.	Date	Scale @ Arch E1
1858	04/12/13	NTS

Number	Revision
40.01	00

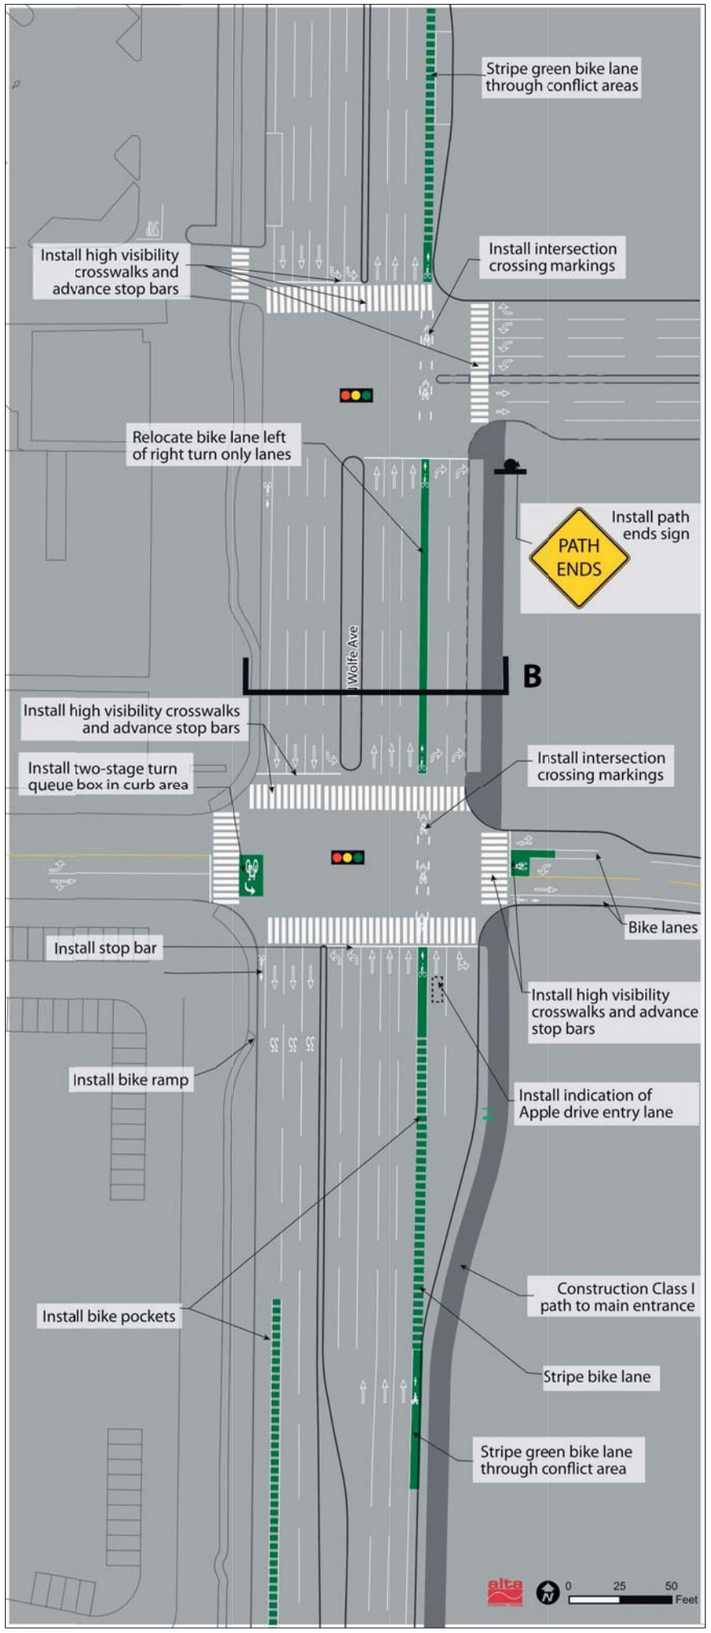

Cross Section B: North Wolfe Road

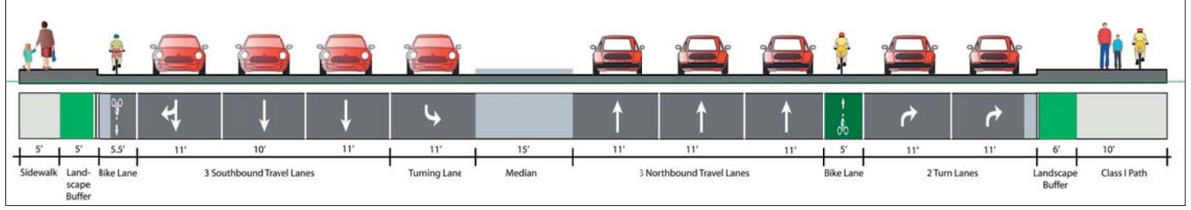

General Notes
1. Do not scale drawings. Dimensions govern.
2. All dimensions are in feet and inches unless noted otherwise.
3. All dimensions shall be verified on site before proceeding with the work.
4. Foster + Partners shall be notified in writing of any discrepancies.
5. Any areas indicated on this sheet are approximate and indicative only.

Rev.	Date	Reason For Issue	Chk
00	04/12/13	Planning Revision 06	

Key Plan

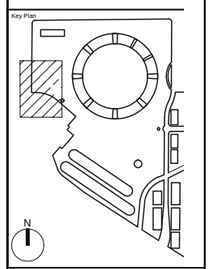

Foster + Partners
Riverside, 22 Hester Road
London SW11 4AN
T +44 (0)20 7738 0455
F +44 (0)20 7738 1027
© Foster + Partners 2010

ARUP
Arup North America Ltd.
560 Mission Street, Suite 700
San Francisco, CA 94105 USA
Tel (415) 957 9445 Fax (415) 957 9096
www.arup.com

OLIN
LANDSCAPE ARCHITECTURE AND URBAN DESIGN
PUBLIC LEDGER BUILDING,SUITE 1123
150 SOUTH INDEPENDENCE MALL WEST
PHILADELPHIA, PA 19106
TEL 215.440.0030 / FAX 215.440.0041
WWW.THEOLINSTUDIO.COM
OLIN PARTNERSHIP, LTD.

KIER & WRIGHT
3350 Scott Boulevard, Building 22
Santa Clara, California 95054
Phone: (408) 727 6665 Fax: (408) 727 5641
www.kierwright.com
© Kier & Wright, 2011

alta
2560 9th Street, Suite 212
Berkeley, CA 94710
p:510.540.5008 f:510.540.5039
www.altaplanning.com

Client
Apple Inc.

Project
Apple Campus 2

Title
Perimeter Bicycle Strategy

Project No.	Date	Scale @ Arch E1
1858	04/12/13	NTS

Number	Revision
40.02	00

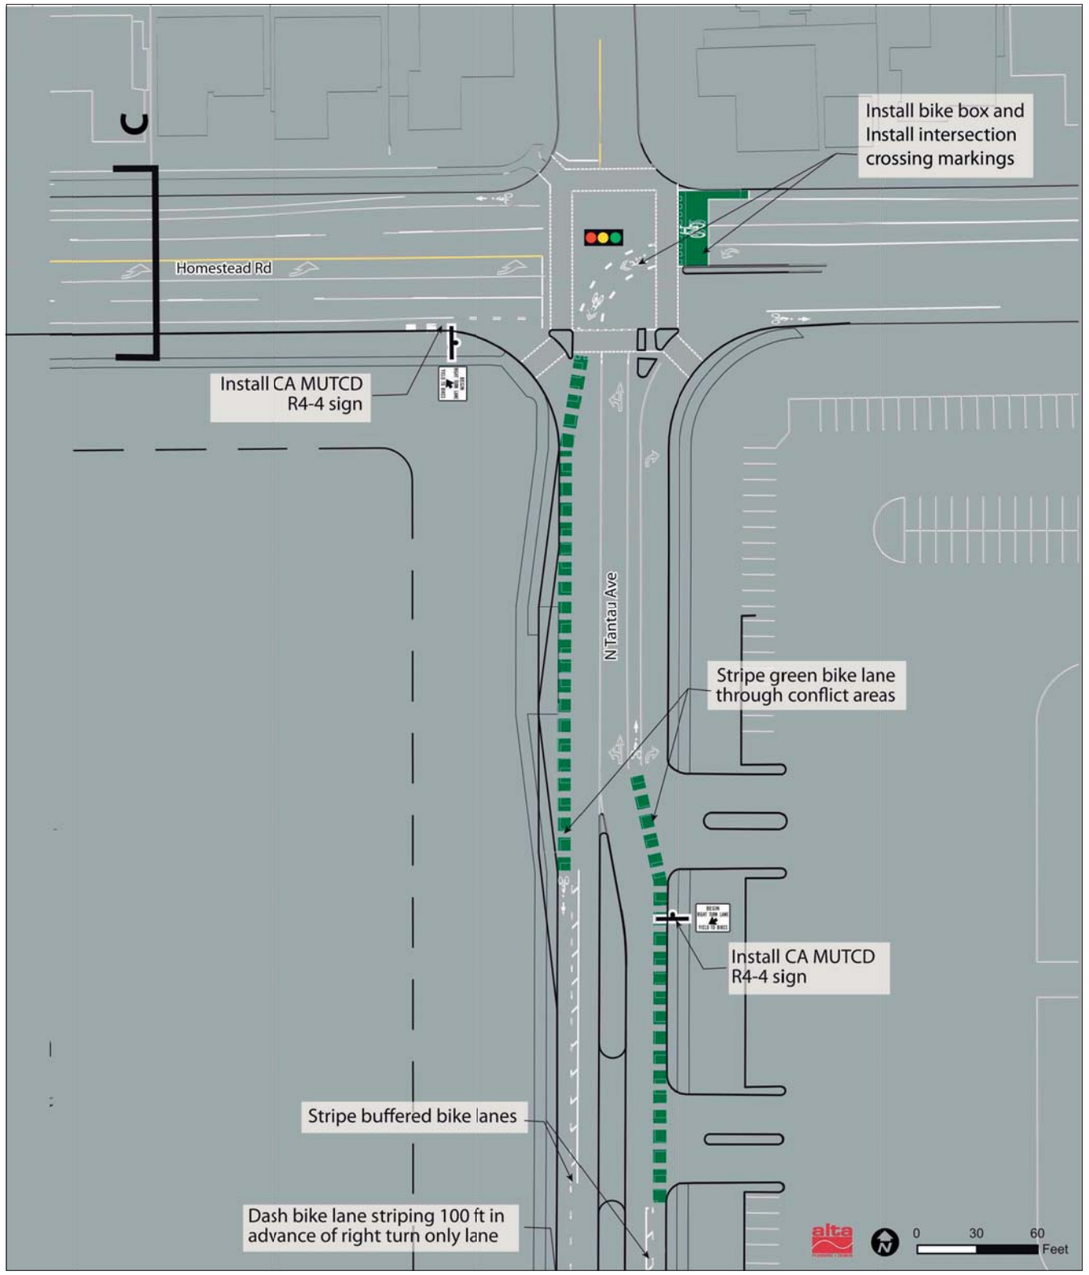

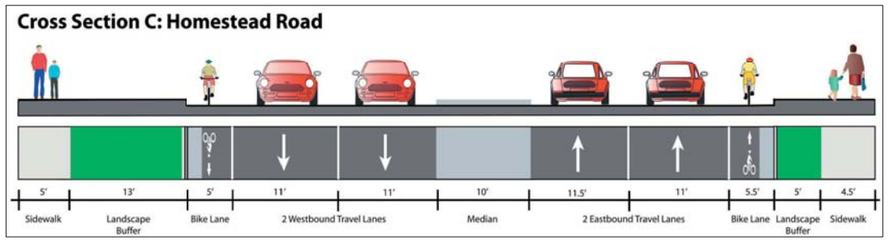

General Notes

1. Do not scale drawings. Dimensions govern.
2. All dimensions are in feet and inches unless noted otherwise.
3. All dimensions shall be verified on site before proceeding with the work.
4. Foster + Partners shall be notified in writing of any discrepancies.
5. Any areas indicated on this sheet are approximate and indicative only.

Rev.	Date	Reason For Issue	Chk
00	04/12/13	Planning Revision 06	

Key Plan

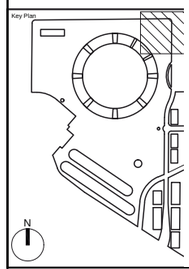

Foster + Partners
Riverside, 22 Hester Road
London SW11 4AN
T +44 (0)20 7738 0455
F +44 (0)20 7738 1027

© Foster + Partners 2010

ARUP
Arup North America Ltd.
560 Mission Street, Suite 700
San Francisco, CA 94105 USA
Tel +415 567 8445 Fax +415 567 9056
www.arup.com

OLIN
LANDSCAPE ARCHITECTURE AND URBAN DESIGN
PUBLIC LEDGER BUILDING,SUITE 1123
150 SOUTH INDEPENDENCE MALL WEST
PHILADELPHIA, PA 19106
TEL 215.440.0030 / FAX 215.440.0041
WWW.THEOLINSTUDIO.COM
OLIN PARTNERSHIP, LTD.

KIER & WRIGHT
3350 Scott Boulevard, Building 22
Santa Clara, California 95054
Phone: (408) 727 6665 Fax: (408) 727 5641
www.kierwright.com

© Kier & Wright, 2011

alta
2560 9th Street, Suite 212
Berkeley, CA 94710
p:510.540.5008 f:510.540.5039
www.altaplanning.com

Client
Apple Inc.

Project
Apple Campus 2

Title
Perimeter Bicycle Strategy

Project No.	Date	Scale @ Arch E1
1858	04/12/13	NTS

Number	Revision
40.03	00

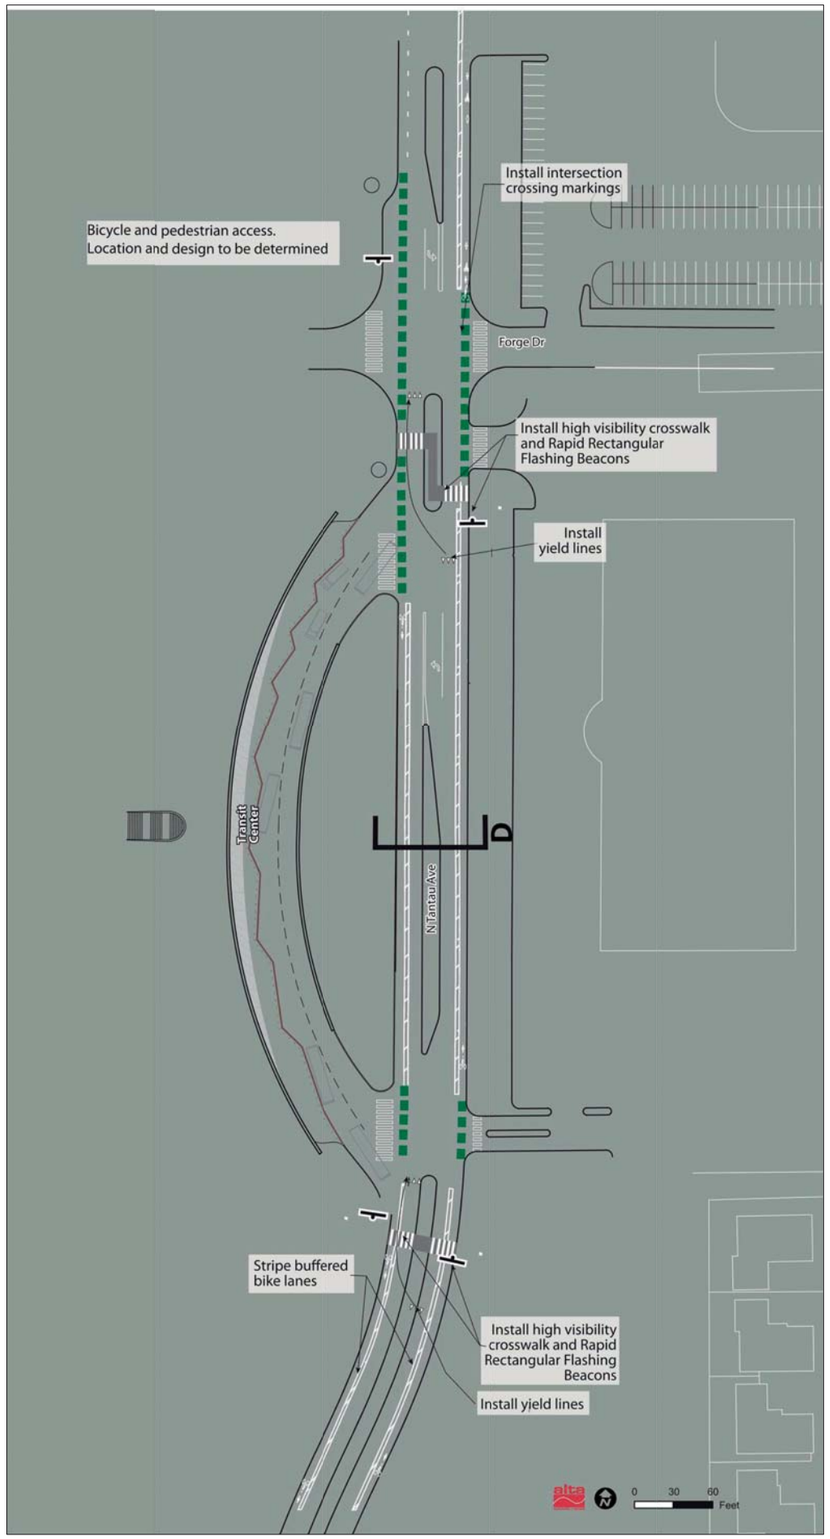

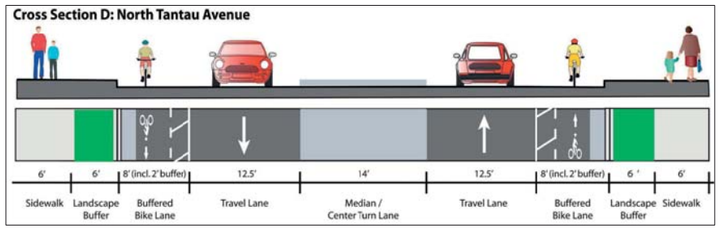

General Notes

1. Do not scale drawings. Dimensions govern.
2. All dimensions are in feet and inches unless noted otherwise.
3. All dimensions shall be verified on site before proceeding with the work.
4. Foster + Partners shall be notified in writing of any discrepancies.
5. Any areas indicated on this sheet are approximate and indicative only.

Rev.	Date	Reason For Issue	Chk
00	04/12/13	Planning Revision 06	

Key Plan

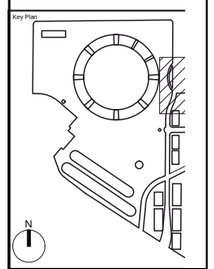

Foster + Partners
Riverside, 22 Hester Road
London SW11 4AN
T +44 (0)20 7738 0455
F +44 (0)20 7738 1107

© Foster + Partners 2010

ARUP
Arup North America Ltd.
560 Mission Street, Suite 700
San Francisco, CA 94105 USA
Tel (415) 957 9445 Fax (415) 957 9096
www.arup.com

OLIN
LANDSCAPE ARCHITECTURE AND URBAN DESIGN
PUBLIC LEDGER BUILDING,SUITE 1123
150 SOUTH INDEPENDENCE MALL WEST
PHILADELPHIA, PA 19106
TEL 215.440.0030 / FAX 215.440.0041
WWW.THEOLINSTUDIO.COM
OLIN PARTNERSHIP, LTD.

KIER & WRIGHT
3350 Scott Boulevard, Building 22
Santa Clara, California 95054
Phone: (408) 727 6665 Fax: (408) 727 5641
www.kierwright.com © Kier & Wright, 2011

alta
www.altaplanning.com
2560 9th Street, Suite 212
Berkeley, CA 94710
p:510.540.5008 f:510.540.5039

Client
Apple Inc.

Project
Apple Campus 2

Title
Perimeter Bicycle Strategy

Project No.	Date	Scale @ Arch E1
1858	04/12/13	NTS

Number	Revision
40.04	00

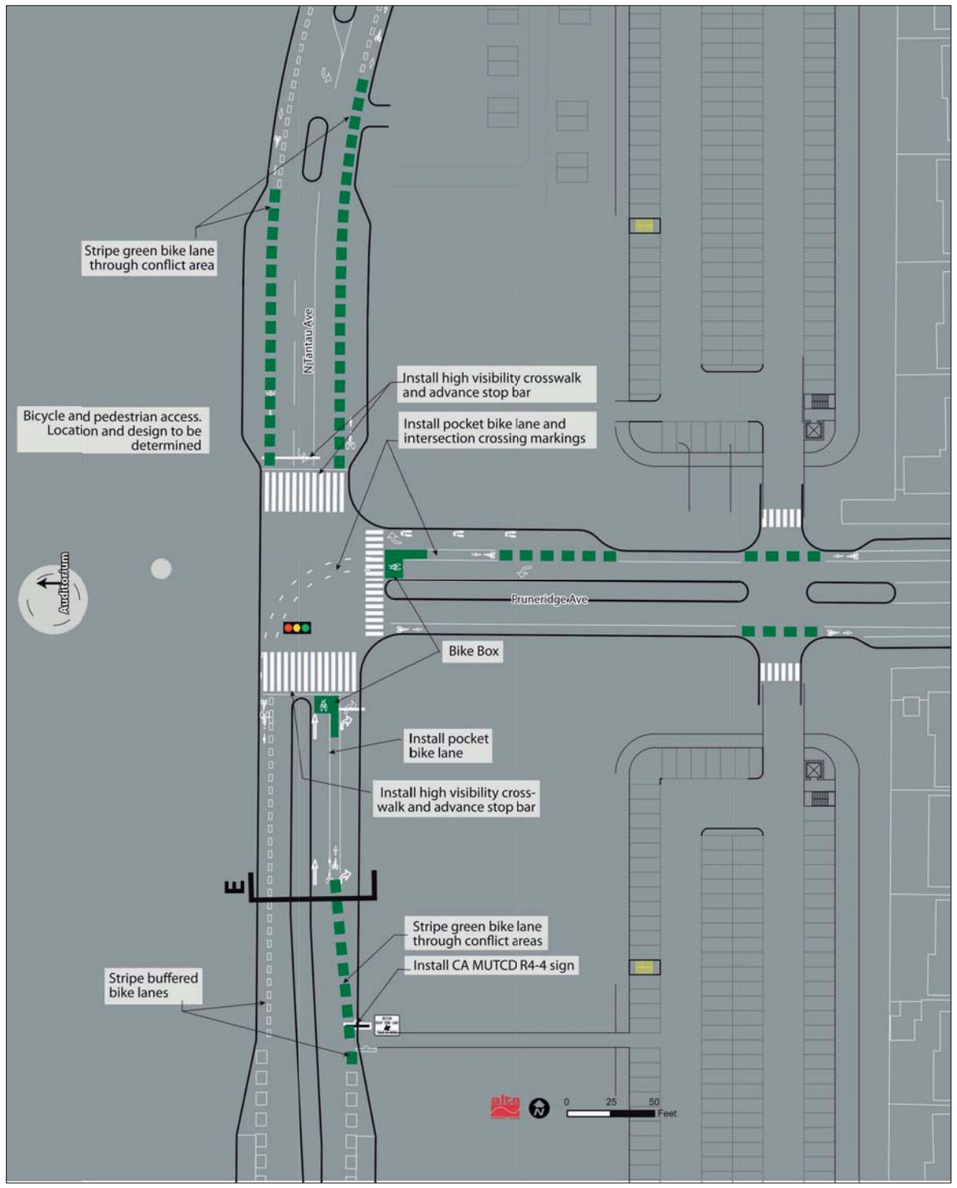

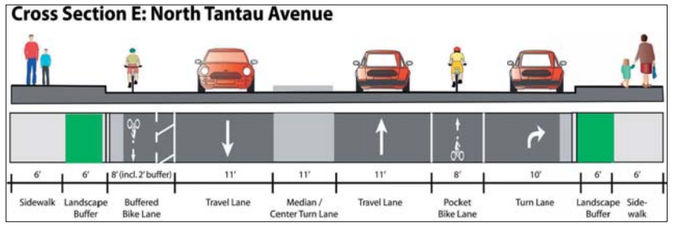

General Notes

1. Do not scale drawings. Dimensions govern.
2. All dimensions are in feet and inches unless noted otherwise.
3. All dimensions shall be verified on site before proceeding with the work.
4. Foster + Partners shall be notified in writing of any discrepancies.
5. Any areas indicated on this sheet are approximate and indicative only.

Rev.	Date	Reason For Issue	Chk
00	04/12/13	Planning Revision 06	

Key Plan

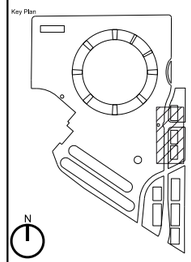

Foster + Partners

Riverside, 22 Hester Road
London SW11 4AN
T +44 (0)20 7738 0455
F +44 (0)20 7738 1107

© Foster + Partners 2010

ARUP

Arup North America Ltd.
560 Mission Street, Suite 700
San Francisco, CA 94105 - USA
Tel (415) 957 9445 , Fax (415) 957 9096
www.arup.com

OLIN

LANDSCAPE ARCHITECTURE AND URBAN DESIGN
PUBLIC LEDGER BUILDING,SUITE 1123
150 SOUTH INDEPENDENCE MALL WEST
PHILADELPHIA, PA 19106
TEL 215.440.0030 / FAX 215.440.0041
WWW.THEOLINSTUDIO.COM
OLIN PARTNERSHIP, LTD.

KIER & WRIGHT

3350 Scott Boulevard, Building 22
Santa Clara, California 95054
Phone: (408) 727 6665 Fax: (408) 727 5641
www.kierwright.com

© Kier & Wright, 2011

alta planning + design
www.altaplanning.com
2560 9th Street, Suite 212
Berkeley, CA 94710
p.510.540.5008 f.510.540.5039

Client
Apple Inc.

Project
Apple Campus 2

Title
Perimeter Bicycle Strategy

Project No.	Date	Scale @ Arch E1
1858	04/12/13	NTS

Number	Revision
40.05	00

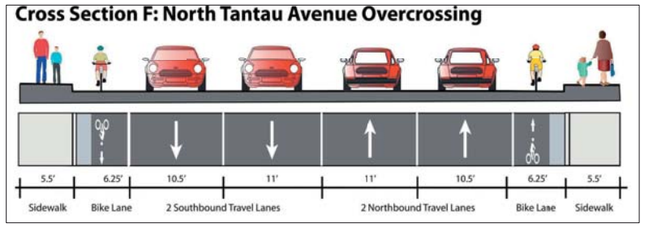

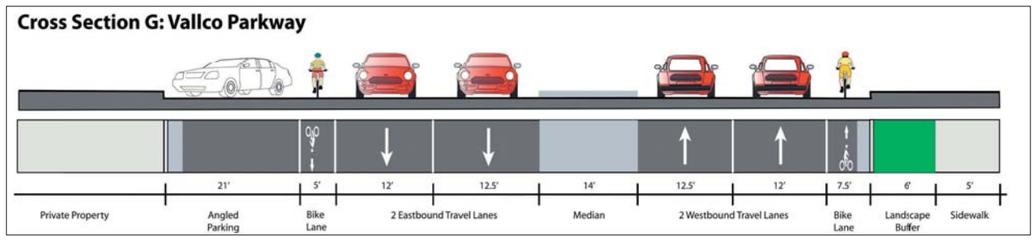

General Notes

1. Do not scale drawings. Dimensions govern.
2. All dimensions are in feet and inches unless noted otherwise.
3. All dimensions shall be verified on site before proceeding with the work.
4. Foster + Partners shall be notified in writing of any discrepancies.
5. Any areas indicated on this sheet are approximate and indicative only.

Rev.	Date	Reason For Issue	Chk
00	04/12/13	Planning Revision 06	

Key Plan

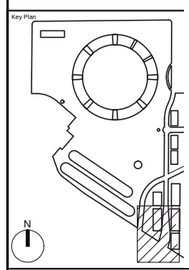

Foster + Partners
Riverside, 22 Hester Road
London SW11 4AN
T +44 (0)20 7738 0455
F +44 (0)20 7738 1107

© Foster + Partners 2010

ARUP
Arup North America Ltd.
560 Mission Street, Suite 700
San Francisco, CA 94105 USA
Tel (415) 957 9445 Fax (415) 957 9096
www.arup.com

OLIN
LANDSCAPE ARCHITECTURE AND URBAN DESIGN
PUBLIC LEDGER BUILDING,SUITE 1123
150 SOUTH INDEPENDENCE MALL WEST
PHILADELPHIA, PA 19106
TEL 215.440.0030 / FAX 215.440.0041
WWW.THEOLINSTUDIO.COM
OLIN PARTNERSHIP, LTD.

KIER & WRIGHT
3350 Scott Boulevard, Building 22
Santa Clara, California 95054
Phone: (408) 727 6665 Fax: (408) 727 5641
www.kierwright.com © Kier & Wright, 2011

alta
2560 9th Street, Suite 212
Berkeley, CA 94710
p:510.540.5008 f:510.540.5039
www.altaplanning.com

Client
Apple Inc.

Project
Apple Campus 2

Title
Perimeter Bicycle Strategy

Project No.	Date	Scale @ Arch E1
1858	04/12/13	NTS

Number	Revision
40.06	00

$$$$SYSTIME$$$
$$$$DWG$$$