Building Inspection Division
THESE PLANS HAVE BEEN REVIEWED FOR COMPLIANCE WITH THE CURRENT EDITION OF THE FLORIDA BUILDING CODE
Date: 11/15/19
Permit Number: BLD19-06035

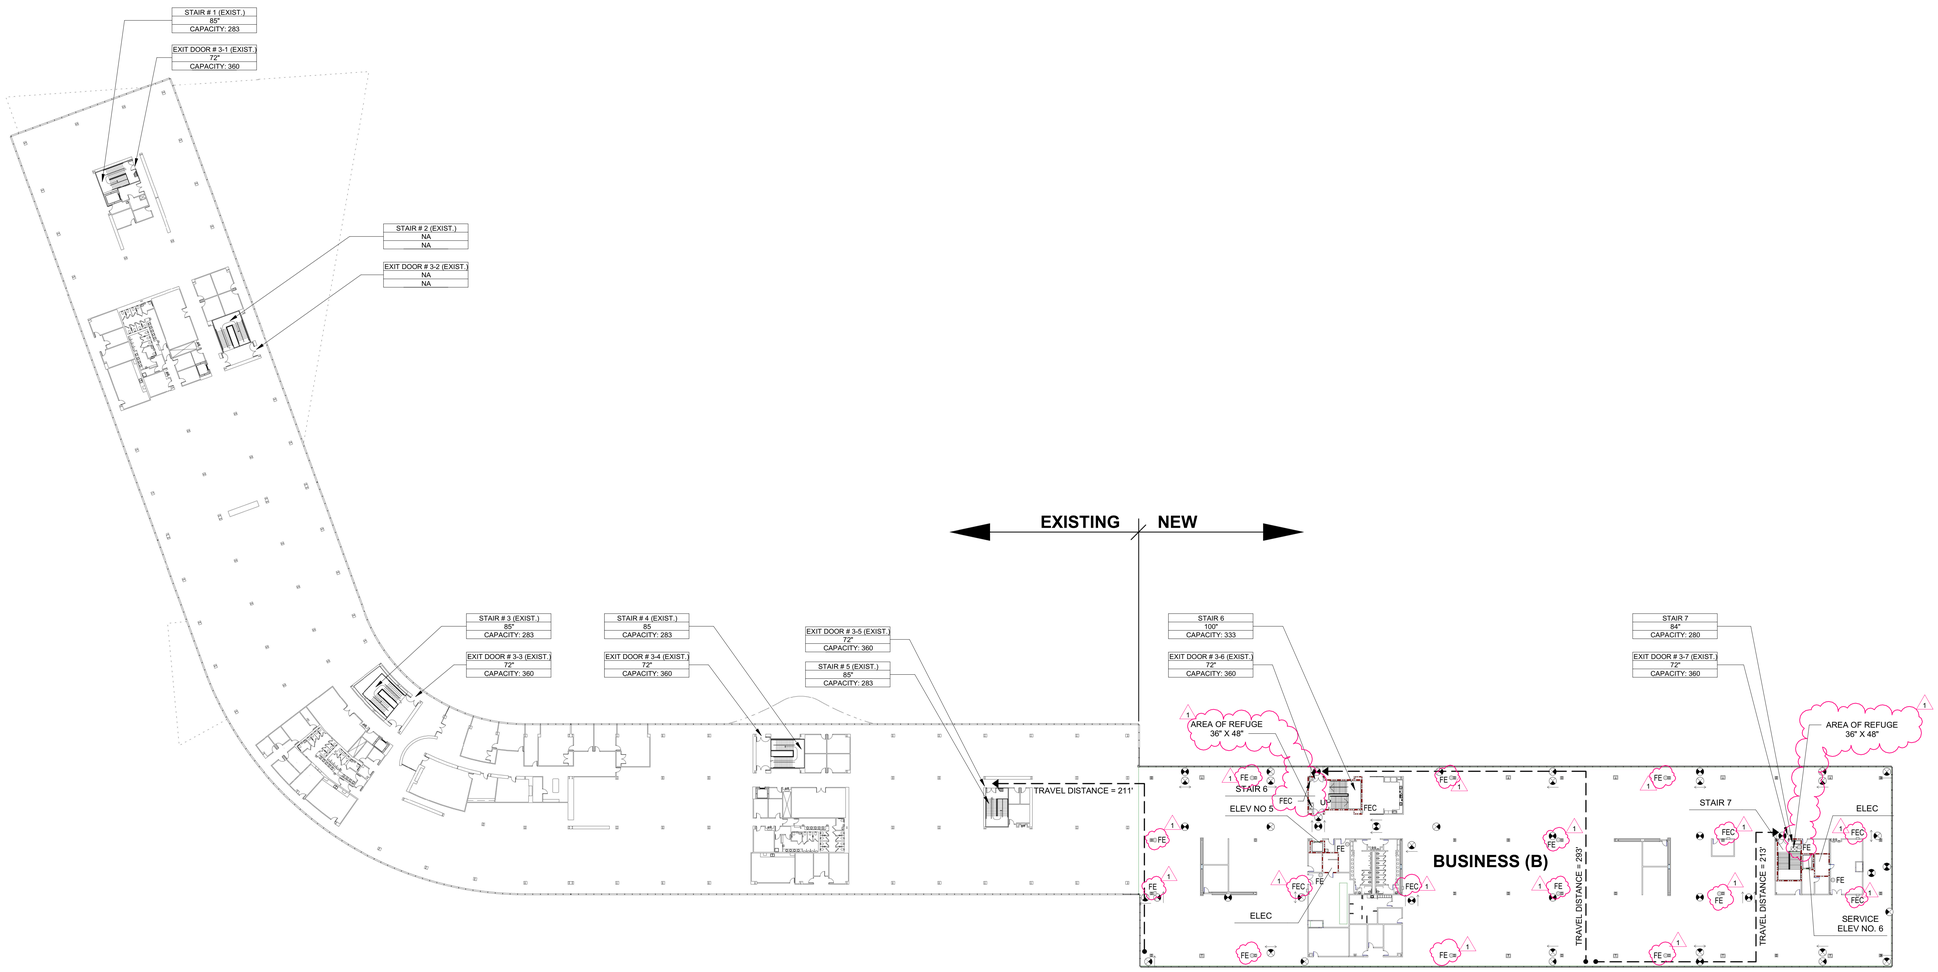

LIFE SAFETY LEGEND

EXIT N0.
WIDTH
CAPACITY
LIFE SAFETY TAG

DISTANCE
TRAVEL PATH

EXIT LIGHT

FE
FIRE EXTINGUISHER - SURFACE MOUNTED

FEC
FIRE EXTINGUISHER CABINET

ACCESSIBLE ROUT

ACCESSIBLE PARKING

1 HOUR FIRE RATING
2-HOUR FIRE RATING
3-HOUR FIRE RATING
SMOKE BARRIER (1-HOUR RATED)
SMOKE PARTITION (NON-RATED)
ASSUMED PROPERTY LINE

1 **LIFE SAFETY - LEVEL 3**
Scale: 1" = 40'-0"

SCALE: 1" = 40'-0" 0 20' 40' 80' 120'

N TN

LEVEL 3 EXIT CALCULATIONS EXISTING AND NEW	AREA (SF)	LOAD FACTOR (SF PER PERSON)	OCCUPANCY LOAD	EXIT (UNITS IN INCHES) REQUIRED DOOR (0.2)	REQUIRED STAIR (0.3)	PROVIDED DOOR (0.2)	PROVIDED STAIR (0.3)	No. Exits Required (FBC 1006.2.1.1)	No. Exits Provided
BUSINESS (EXISTING)	108,900	100	1,089						
BUSINESS	**64,743**	**100**	**648**						
TOTAL:	**173,643**		**1,737**	**348**	**522**	**432**	**524**	**4**	**6**

EXIT CALCULATIONS - LEVEL 3

Project Management Initials:
Designer: Designer Checker: Checker Approved: Approver/ARCH E1 30"x42"

Last Plotted: 9/30/2019 6:15:18 PM
Filename: BM 360/60601397-Publix HQ/60601397_Publix HQ_ARCH_E3019.rvt

Printed on ___% Post-Consumer Recycled Content Paper

This drawing has been prepared for the use of AECOM's client and may not be used, reproduced or relied upon by third parties, except as agreed by AECOM and its client, as required by law or for use by governmental reviewing agencies. AECOM accepts no responsibility, and denies any liability whatsoever to any party that modifies this drawing without AECOM's express written consent. Do not scale this document. All measurements must be obtained from the stated dimensions.

AECOM
BATSON-COOK CONSTRUCTION

PROJECT

PUBLIX HEADQUARTERS BUILDING ADDITION AND PARKING LOT EXPANSION

3300 PUBLIX CORPORATE PARKWAY
LAKELAND, FL 33811

CLIENT

Publix

3300 PUBLIX CORPORATE PARKWAY
LAKELAND, FL 33811

www.publix.com

CONSULTANT

AECOM

AECOM TECHNICAL SERVICES, INC.
800 Douglas Entrance
North Tower, 2nd Floor
Coral Gables, FL 33134
305.444.4691 tel 305.447.3580 fax
www.aecom.com

ARCHITECTURE
LICENSE NO. AA26000687

ENGINEERING
CA LIC. NO. 8115

www.aecom.com

REGISTRATION

STATE OF FLORIDA
STEPHEN PANZARINO
AR92622
REGISTERED ARCHITECT

STEPHEN PANZARINO, REGISTERED ARCHITECT, STATE OF FLORIDA, LICENSE NO. AR92622

THIS ITEM HAS BEEN DIGITALLY SIGNED AND SEALED BY STEPHEN PANZARINO, REGISTERED ARCHITECT, STATE OF FLORIDA, LICENSE NO. AR92622 ON THE DATE INDICATED HERE. PRINTED COPIES OF THIS DOCUMENT ARE NOT CONSIDERED SIGNED AND SEALED AND THE SIGNATURE MUST BE VERIFIED ON ANY ELECTRONIC COPIES

Panzarino, Stephen
Digitally signed by Panzarino, Stephen
DN: CN=Panzarino, Stephen, OU=USTPA1, OU=US, OU=AMER, OU=AECOMUsers, DC=na, DC=aecomnet, DC=com
Date: 2019.09.30 16:29:57-04'00'

NOTICE: THE OFFICIAL RECORD OF THIS SHEET IS THE ELECTRONIC FILE SIGNED AND SEALED UNDER RULE 61G1-16.005 F.A.C.

ISSUE/REVISION

I/R	DATE	DESCRIPTION
1	SEP 30, 2019	100% CONSTRUCTION DOCUMENTS
0	AUG 23, 2019	CONSTRUCTION DOCUMENTS
	MAY 31, 2019	35% DESIGN COMPLETION
	MAY 01, 2019	ISSUED FOR APPROVAL

PROJECT NUMBER

60601397

SHEET TITLE

LIFE SAFETY - LEVEL 3

SHEET NUMBER

A0-2-30

©2016 AECOM Corporation