Building Inspection Division
THESE PLANS HAVE BEEN REVIEWED FOR COMPLIANCE WITH THE CURRENT EDITION OF THE FLORIDA BUILDING CODE
Date: 11/15/19
Permit Number: BLD19-06035

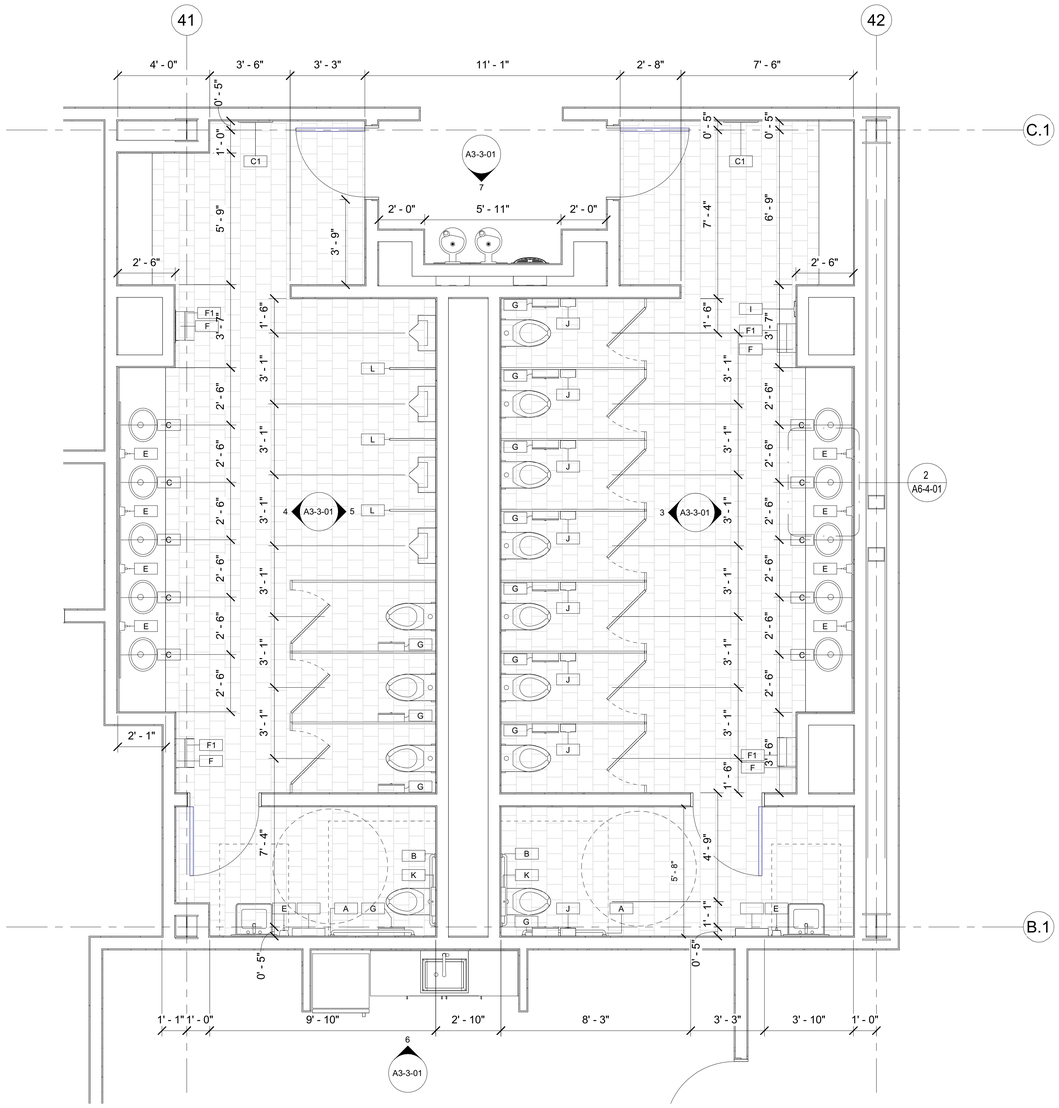

1 RESTROOM PLAN LEVEL 1 (shown)
Scale: 3/8" = 1'-0"
SCALE: 3/8" = 1'-0"

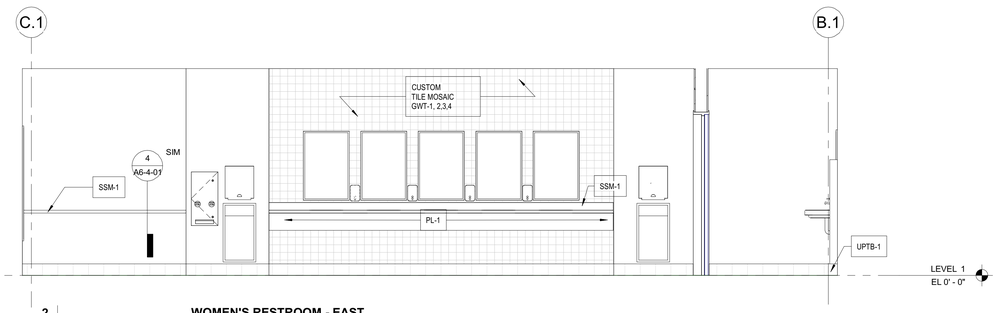

2 WOMEN'S RESTROOM - EAST
Scale: 3/8" = 1'-0"
SCALE: 3/8" = 1'-0"

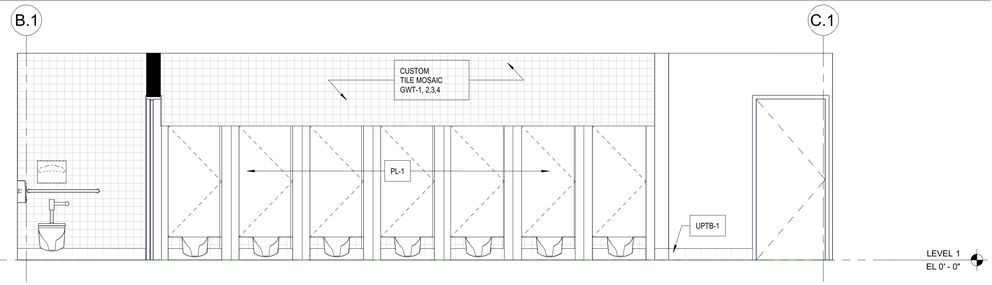

3 WOMEN'S RESTROOM - WEST
Scale: 3/8" = 1'-0"
SCALE: 3/8" = 1'-0"

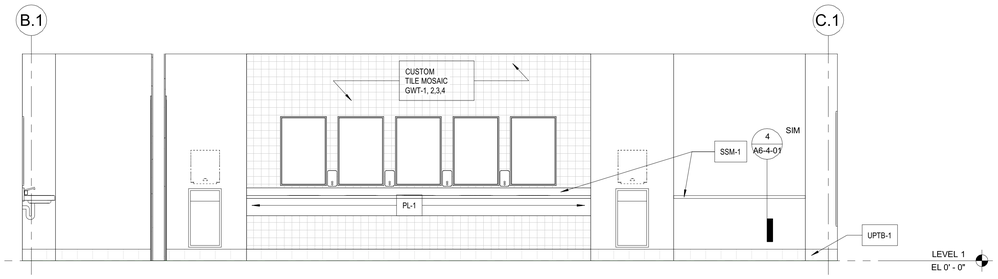

4 MEN'S RESTROOM - EAST
Scale: 3/8" = 1'-0"
SCALE: 3/8" = 1'-0"

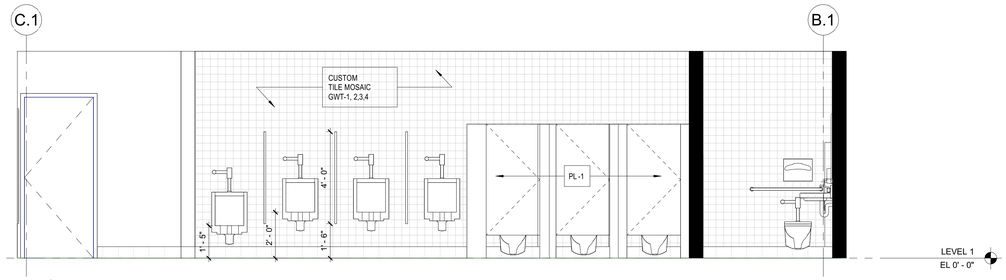

5 MEN'S RESTROOM - WEST
Scale: 3/8" = 1'-0"
SCALE: 3/8" = 1'-0"

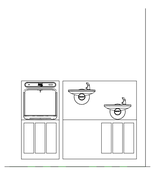

7 WATER FOUNTAIN
Scale: 3/8" = 1'-0"
SCALE: 3/8" = 1'-0"

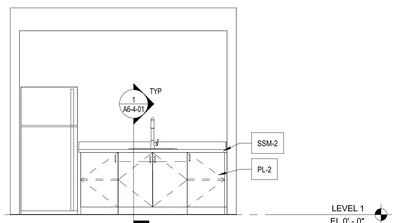

6 MOTHER'S ROOM MILLWORK
Scale: 3/8" = 1'-0"
SCALE: 3/8" = 1'-0"

STANDARD TOILET ACCESSORY MOUNTING HEIGHTS

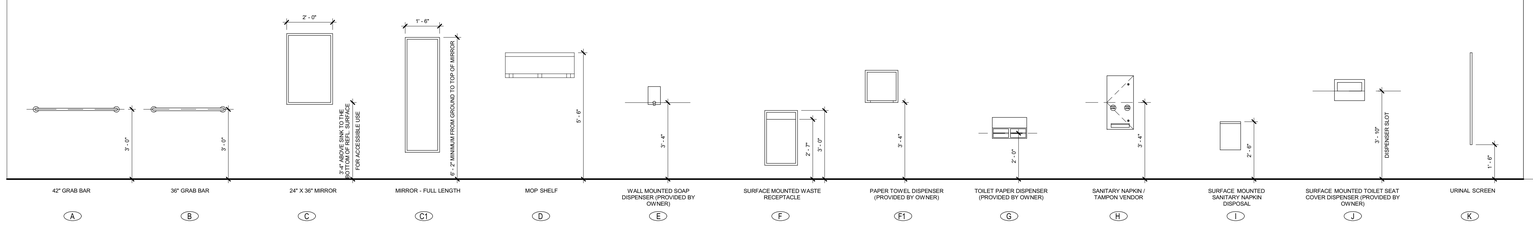

acm_Accessible Toilet Clearances
Scale: 3/8" = 1'-0"
SCALE: 3/8" = 1'-0"

STANDARD TOILET ACCESSORY MOUNTING HEIGHTS

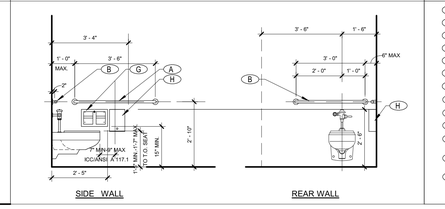

LEGEND

A	42" GRAB BAR
B	36" GRAB BAR
C	24" X 36" MIRROR
C1	FULL LENGTH FRAMED MIRROR
D	MOP SHELF
E	WALL MOUNTED SOAP DISPENSER (PBO.)
F	SURFACE MOUNT WASTE RECEPTACLE
F1	SURFACE MOUNT PAPER TOWEL DISPENSER (PBO)
G	TOILET PAPER DISPENSER
H	SANITARY NAPKIN / TAMPON VENDOR (PBO.)
I	SURFACE MOUNTED SANITARY NAPKIN DISPOSAL (PBO.)
J	SURFACE MOUNTED TOILET SEAT COVER DISPENSER (PBO.)
K	URINAL SCREEN (PBO.)

AECOM
BATSON-COOK CONSTRUCTION

PROJECT
PUBLIX HEADQUARTERS BUILDING ADDITION AND PARKING LOT EXPANSION
3300 PUBLIX CORPORATE PARKWAY
LAKELAND, FL 33811

CLIENT
Publix
3300 PUBLIX CORPORATE PARKWAY
LAKELAND, FL 33811
www.publix.com

CONSULTANT
AECOM
AECOM TECHNICAL SERVICES, INC.
800 Douglas Entrance
North Tower, 2nd Floor
Coral Gables, FL 33134
305.444.4691 tel 305.447.3580 fax
www.aecom.com

ARCHITECTURE
LICENSE NO. AA26000687

ENGINEERING
CA LIC. NO. 8115

www.aecom.com

REGISTRATION
STATE OF FLORIDA
STEPHEN PANZARINO
AR92622
REGISTERED ARCHITECT

STEPHEN PANZARINO, REGISTERED ARCHITECT, STATE OF FLORIDA, LICENSE NO. AR92622

THIS ITEM HAS BEEN DIGITALLY SIGNED AND SEALED BY STEPHEN PANZARINO, REGISTERED ARCHITECT, STATE OF FLORIDA, LICENSE NO. AR92622 ON THE DATE INDICATED HERE. PRINTED COPIES OF THIS DOCUMENT ARE NOT CONSIDERED SIGNED AND SEALED AND THE SIGNATURE MUST BE VERIFIED ON ANY ELECTRONIC COPIES

Panzarino, Stephen
Digitally signed by Panzarino, Stephen
DN: CN=Panzarino, Stephen, OU=USTPA1, OU=US, OU=AMER, OU=AECOMUsers, DC=na, DC=aecomnet, DC=icom
Date: 2019.08.26 17:12:16-04'00'

ISSUE/REVISION

I/R	DATE	DESCRIPTION
0	AUG 23, 2019	CONSTRUCTION DOCUMENTS

PROJECT NUMBER
60601397

SHEET TITLE
ENLARGED RESTROOM PLANS

SHEET NUMBER
A3-3-01

This drawing has been prepared for the use of AECOM's client and may not be used, reproduced or relied upon by third parties, except as agreed by AECOM and its client, as required by law or for use by governmental reviewing agencies. AECOM accepts no responsibility, and denies any liability whatsoever, to any party that modifies this drawing without AECOM's express written consent. Do not scale this document. All measurements must be obtained from the stated dimensions.

NOTICE: THE OFFICIAL RECORD OF THIS SHEET IS THE ELECTRONIC FILE SIGNED AND SEALED UNDER RULE 61G1-16.005 F.A.C.

©2016 AECOM Corporation

Project Management Initials:
Designer: Designer Checked: Checker Approved: ApproverARCH E1 30"x42"
Last Printed: 8/26/2019 4:02:15 PM
Filename: BIM 360://60601397-Publix HQ/60601397_Publix HQ_ARCH_R2019 v4
Printed on ___% Post-Consumer Recycled Content Paper