DEMOLITION PLAN
Approved: DWS ARCH E1 30"x42"
Checked: KMW
Designer: NJR
Project Management Initials:

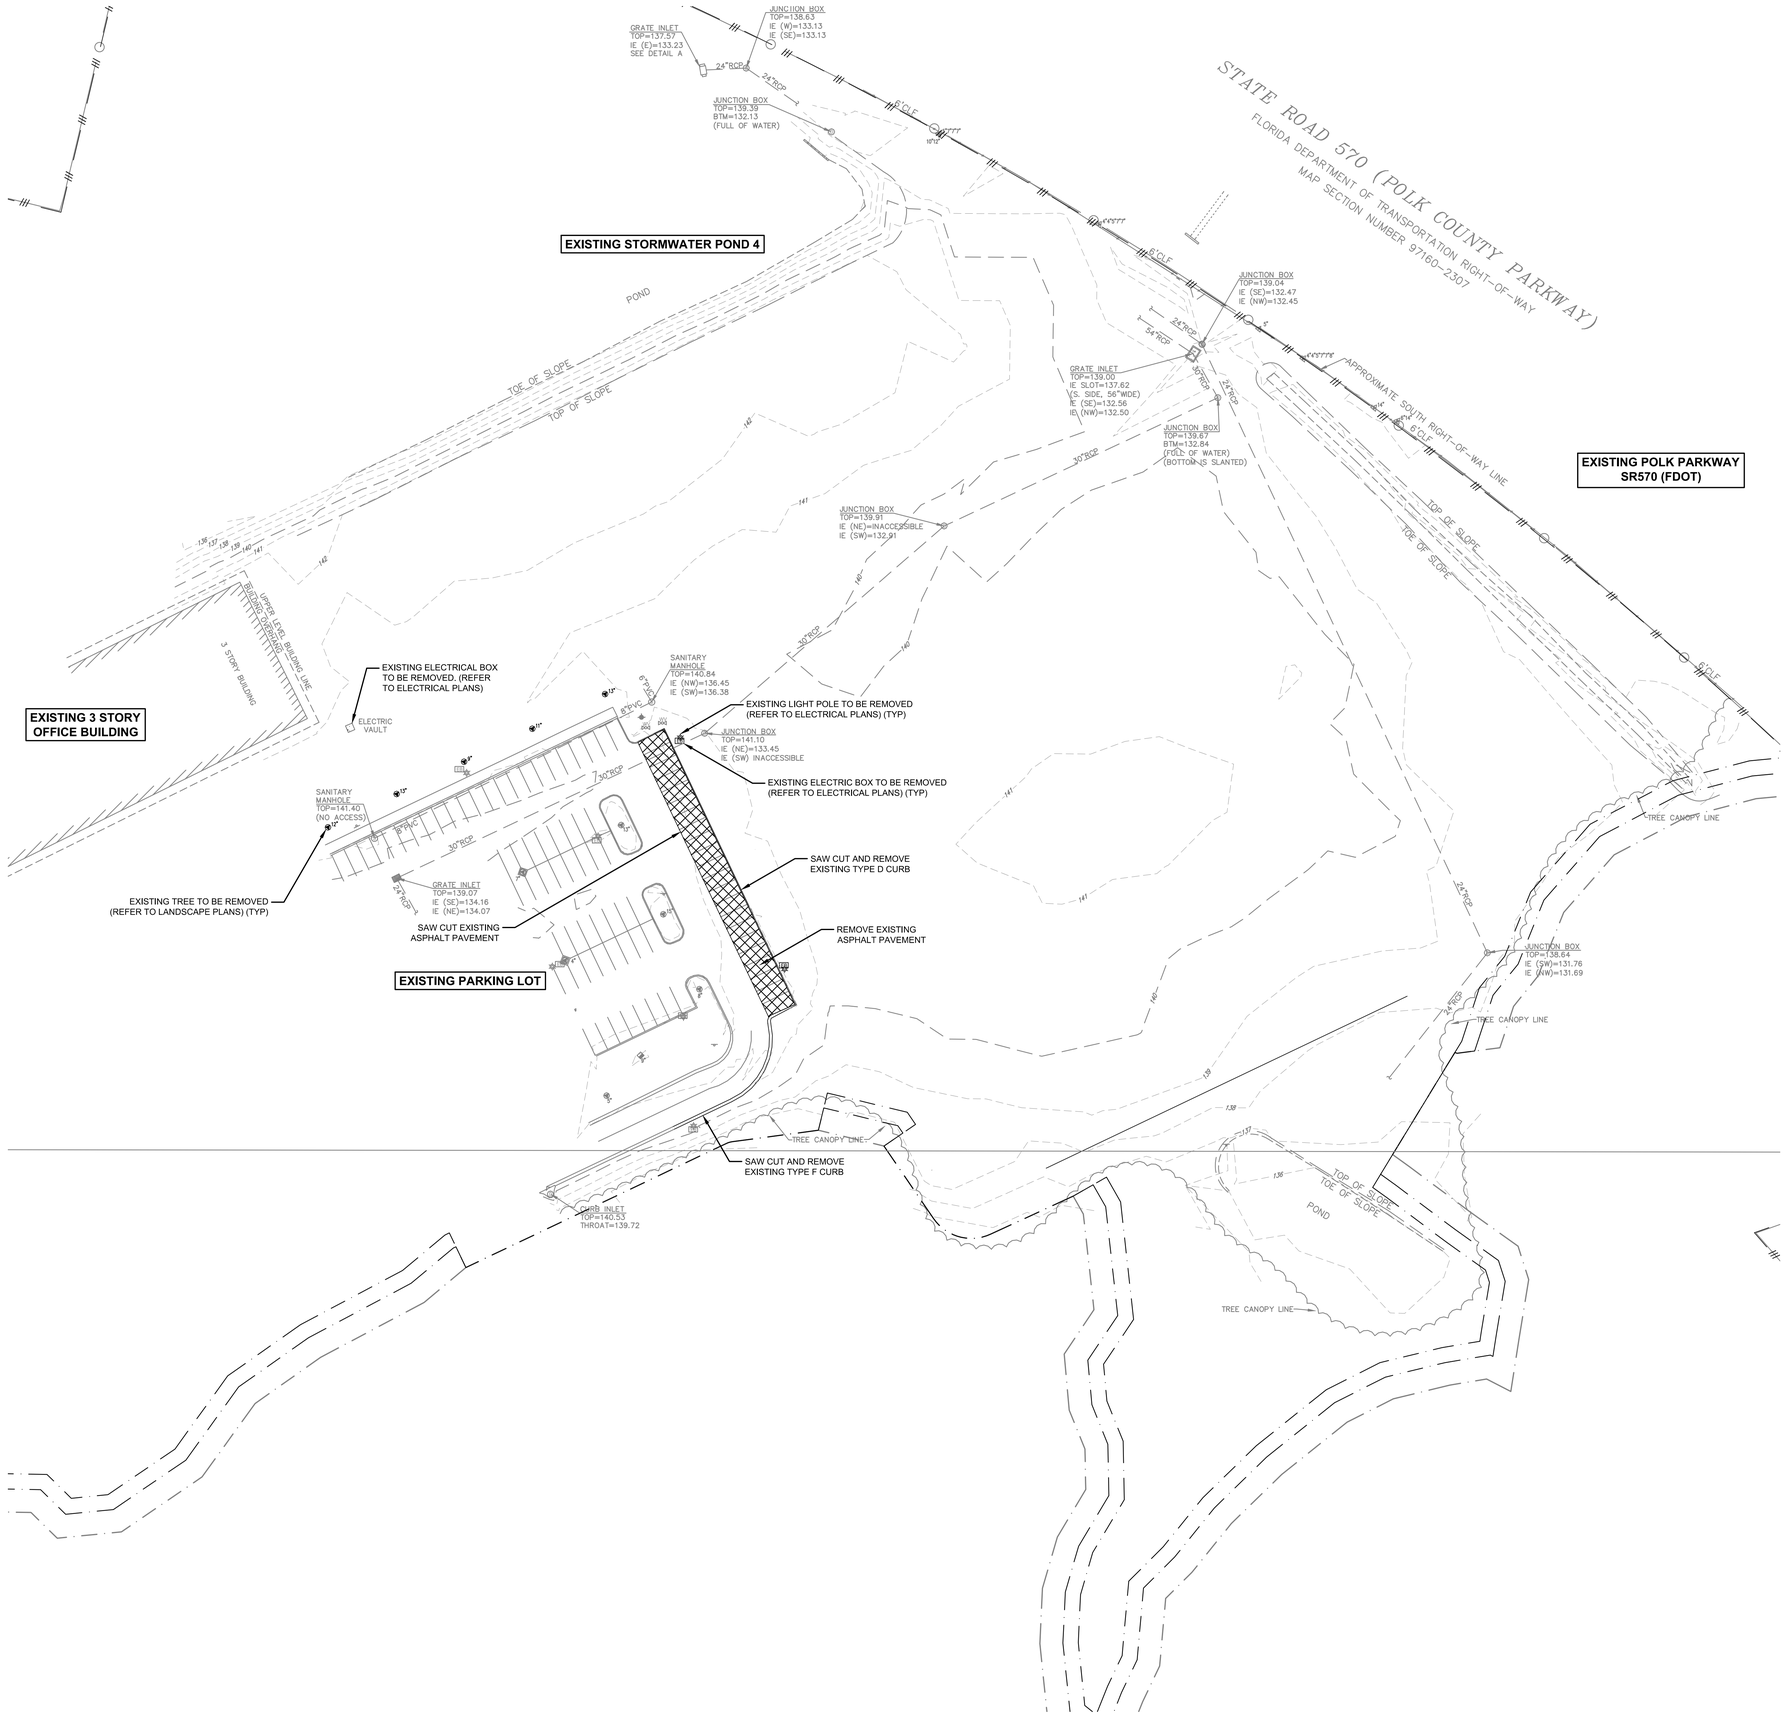

KEY MAP

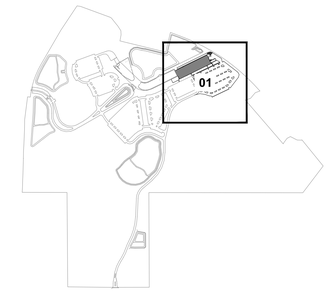

DEMOLITION LEGEND

/// /// ///	PROPERTY LINE
	EXISTING ASPHALT PAVEMENT TO BE REMOVED
	EXISTING CURB TO BE REMOVED
ELECTRIC VAULT	EXISTING ELECTRIC BOX TO BE REMOVED
	EXISTING LIGHT POLE TO BE REMOVED (REFER TO ELECTRICAL PLANS)
	EXISTING ELECTRICAL BOX TO BE REMOVED (REFER TO ELECTRICAL PLANS)
	EXISTING TREE TO BE REMOVED (REFER TO LANDSCAPE PLANS)

NORTH

0 40' 80'
GRAPHIC SCALE

Building Inspection Division
THESE PLANS HAVE BEEN REVIEWED FOR COMPLIANCE WITH THE CURRENT EDITION OF THE FLORIDA BUILDING CODE
Lakeland
Date: 11/15/19
Permit Number: BLD19-06035

AECOM
BATSON-COOK CONSTRUCTION

PROJECT

PUBLIX HEADQUARTERS BUILDING ADDITION AND PARKING LOT EXPANSION

3300 PUBLIX CORPORATE PARKWAY
LAKELAND, FL 33811

CLIENT

Publix

3300 PUBLIX CORPORATE PARKWAY
LAKELAND, FL 33811

www.publix.com

CONSULTANT

AECOM

AECOM TECHNICAL SERVICES, INC.
800 Douglas Entrance
North Tower, 2nd Floor
Coral Gables, FL 33134
305.444.4691 tel 305.447.3580 fax
www.aecom.com

ARCHITECTURE
LICENSE NO. AA26000687

ENGINEERING
CA LIC. NO. 8115

www.aecom.com

Digitally signed by Dennis W Syrja
Date: 2019.08.23 10:45:17 -04'00'

REGISTRATION

DENNIS W. SYRJA LICENSE No. 43423 STATE OF FLORIDA PROFESSIONAL ENGINEER

DENNIS W. SYRJA, P.E.
ENGINEER OF RECORD

NOTICE: THE OFFICIAL RECORD OF THIS SHEET IS THE ELECTRONIC FILE SIGNED AND SEALED UNDER RULE 61G15-23.004, F.A.C.

THIS ITEM HAS BEEN DIGITALLY SIGNED AND SEALED BY DENNIS W. SYRJA, P.E. ON THE DATE ADJACENT TO THE SEAL.

PRINTED COPIES OF THIS DOCUMENT ARE NOT CONSIDERED SIGNED AND SEALED AND THE SIGNATURE MUST BE VERIFIED ON ANY ELECTRONIC COPIES.

ISSUE/REVISION

I/R	DATE	DESCRIPTION
0	AUG 23, 2019	CONSTRUCTION DOCUMENTS

PROJECT NUMBER

60601397

SHEET TITLE

DEMOLITION PLAN

SHEET NUMBER

CD-101

Last Plotted: 8/22/2019 8:21:36 PM
Filename: S:\PROJECTS_CIVIL\PROJECTS\PUBLIX\60_DWG\60_CAD_BIM (CIVIL)\20-SHEETS\CD-101 DEMOLITION PLAN.DWG

Printed on ___% Post-Consumer Recycled Content Paper

©2016 AECOM Corporation