Building Inspection Division
Lakeland
THESE PLANS HAVE BEEN REVIEWED FOR COMPLIANCE WITH THE CURRENT EDITION OF THE FLORIDA BUILDING CODE
Date: 11/15/19
Permit Number: BLD19-06035

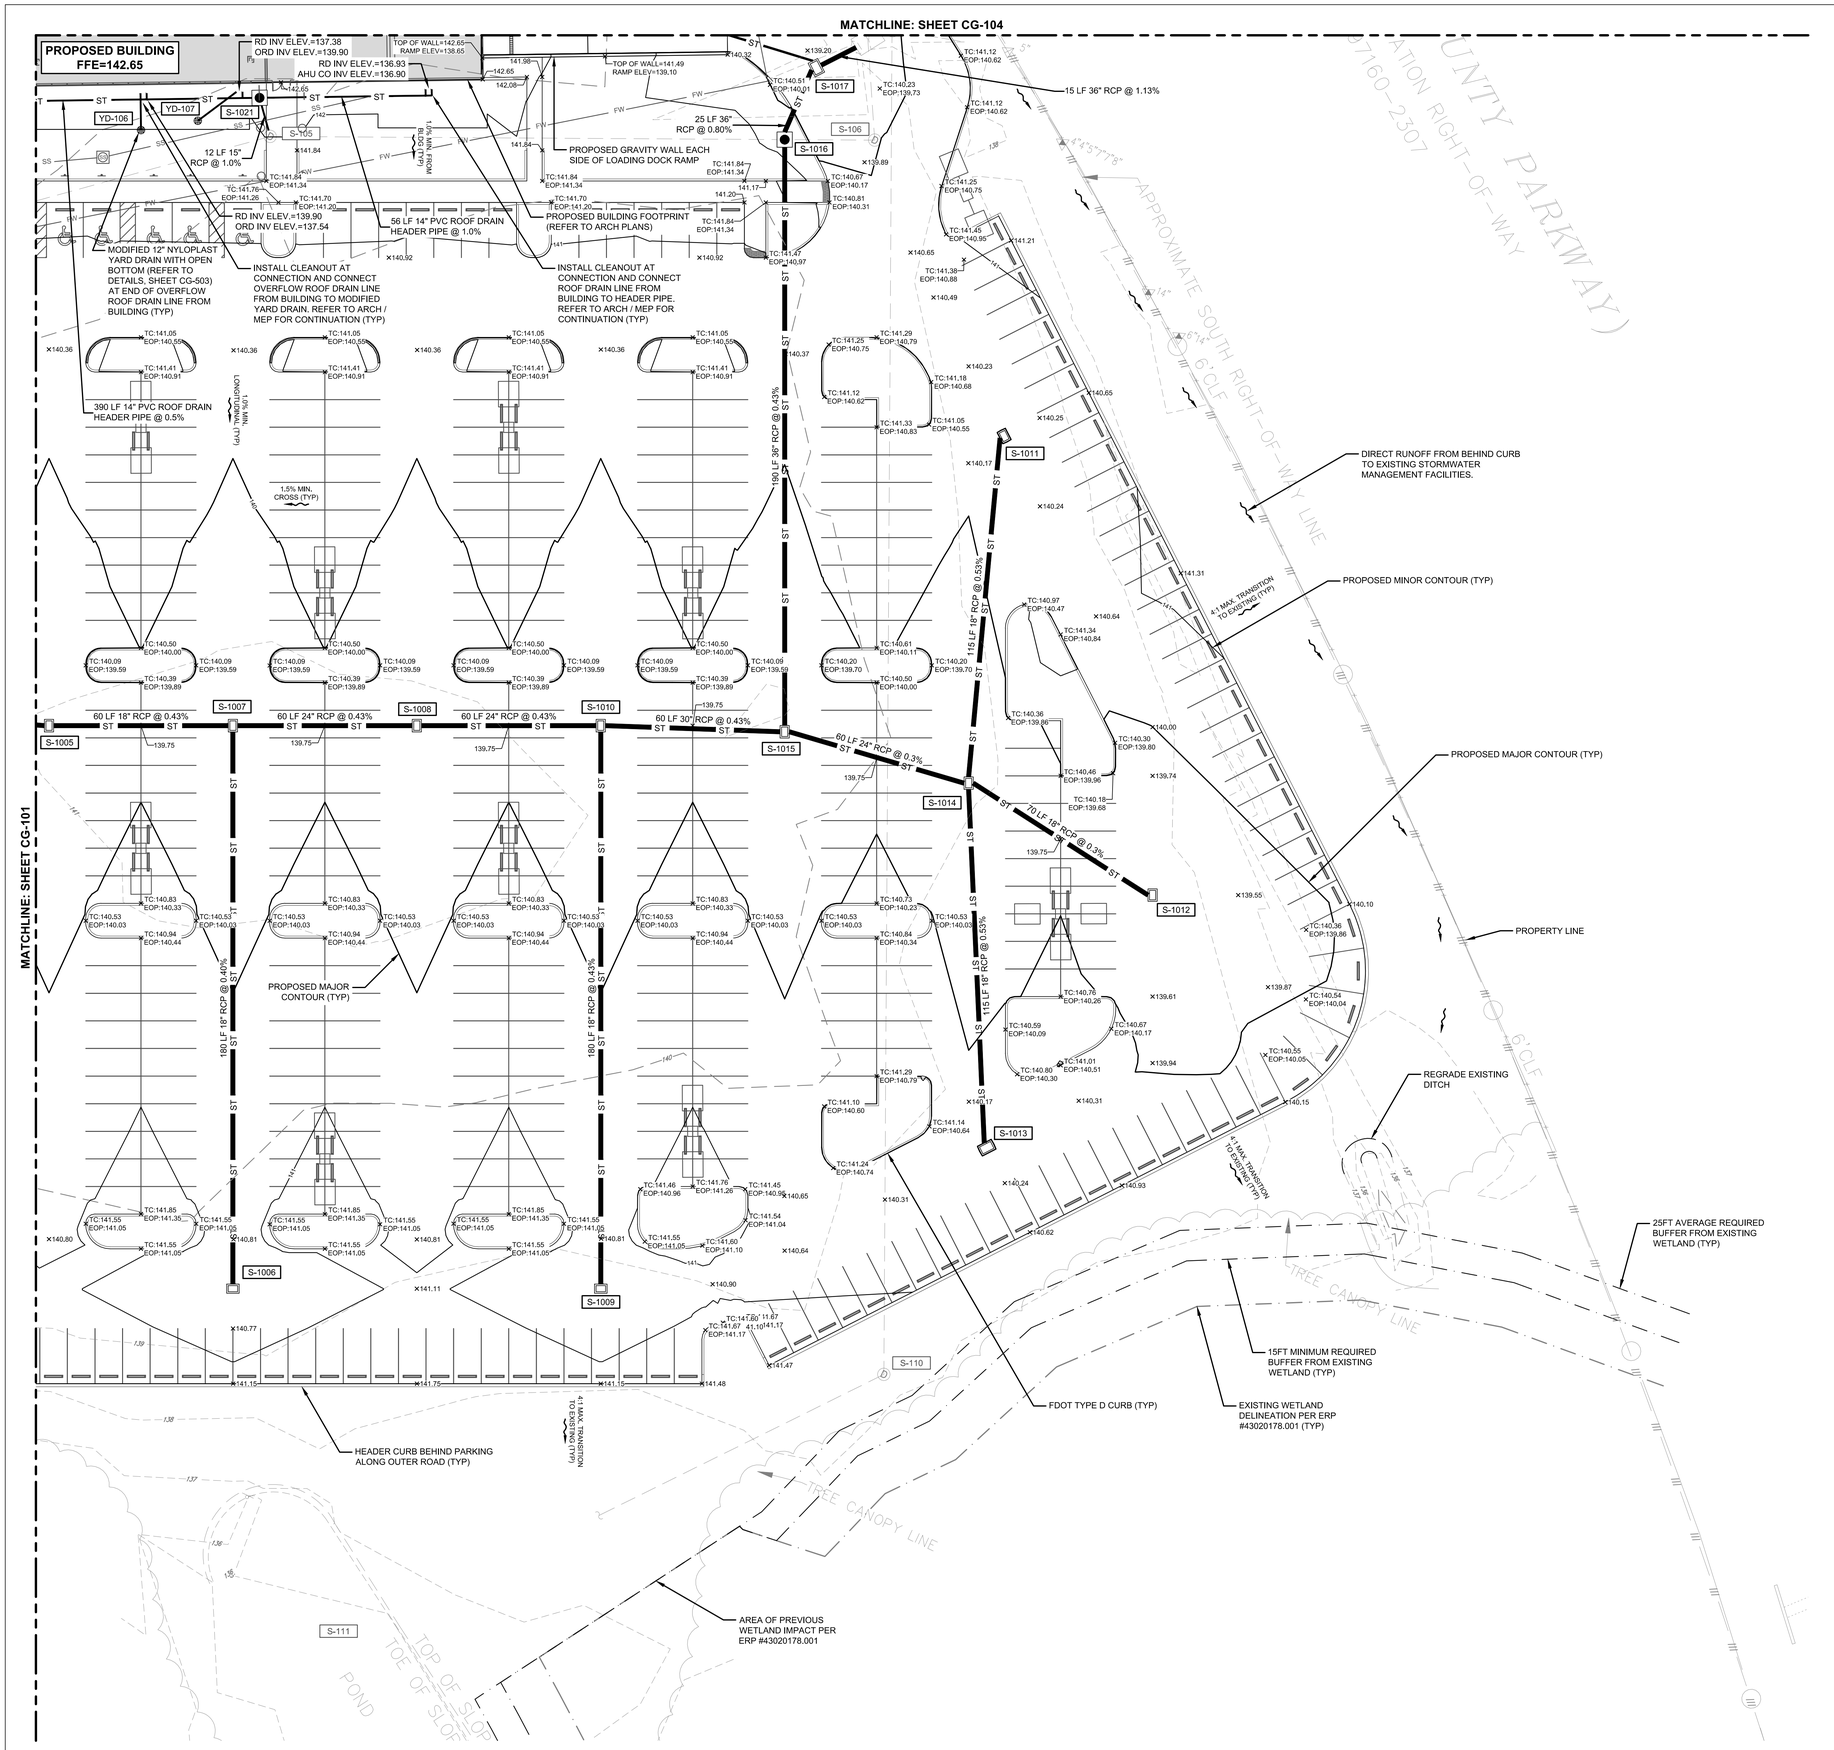

KEY MAP

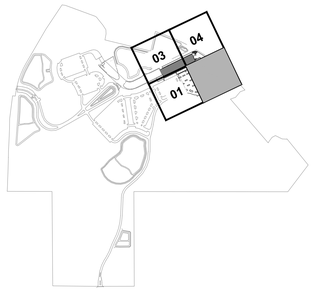

GRADING AND DRAINAGE LEGEND

- PROPERTY LINE
- EXISTING WETLAND JURISDICTION LINE
- WETLAND SETBACK LINE
- EXISTING MAJOR CONTOUR
- EXISTING MINOR CONTOUR
- PROPOSED MAJOR CONTOUR
- PROPOSED MINOR CONTOUR
- PROPOSED STORMWATER YARD DRAIN
- PROPOSED STORMWATER TYPE 'F' INLET
- PROPOSED STORM JUNCTION BOX / PROPOSED STORMWATER JUNCTION BOX
- ×140.83 PROPOSED SPOT ELEVATION
- PROPOSED FLOW DIRECTION

Digitally signed by Dennis W Syrja
Date: 2019.08.23 10:36:44 -04'00'

NOTES:

- REFER TO UTILITY PLANS (SHEETS CU-101 THROUGH CU-104) FOR PROPOSED STORM AND ROOF DRAIN INFORMATION AND ADDITIONAL GRADING DETAIL.
- REFER TO ARCHITECTURAL, MECHANICAL, AND PLUMBING DRAWINGS FOR ADDITIONAL INFORMATION ON PROPOSED ROOF DRAIN AND UTILITY CONNECTION LOCATIONS AND DETAILS.
- REFER TO STRUCTURE TABLE, SHEET CG-104, FOR EXISTING AND PROPOSED STRUCTURE DETAILS.
- REFER TO GRADING AND DRAINAGE DETAILS, SHEETS CG-501 THROUGH CG-504.
- EXISTING STRUCTURE INFORMATION PROVIDED BY TOPOGRAPHIC SURVEY BY POLARIS ASSOCIATES INC. DATED 06/27/19.
- VERTICAL DATUM: NORTH AMERICAN VERTICAL DATUM 1988 (NAVD88). ALL EXISTING AND PROPOSED ELEVATIONS DEPICTED ARE IN FEET NAVD88 (UNLESS OTHERWISE NOTED). TO OBTAIN NATIONAL GEODETIC VERTICAL DATUM 1929 (NGVD29), ADD 0.85 FT TO ELEVATIONS IN NAVD88.
- MAINTAIN MINIMUM HORIZONTAL AND VERTICAL CLEARANCES AT ALL TIMES BETWEEN EXISTING AND PROPOSED FACILITIES. IF MINIMUM CLEARANCES CANNOT BE ACHIEVED, CONTRACTOR SHALL BRING THE CONFLICT TO THE ATTENTION OF THE ENGINEER.
- EXISTING UTILITY AND STORM INFORMATION ARE APPROXIMATE. CONTRACTOR IS RESPONSIBLE FOR FIELD VERIFYING ALL EXISTING CONDITIONS PRIOR TO CONSTRUCTION.

AECOM
BATSON-COOK CONSTRUCTION

PROJECT

PUBLIX HEADQUARTERS BUILDING ADDITION AND PARKING LOT EXPANSION

3300 PUBLIX CORPORATE PARKWAY
LAKELAND, FL 33811

CLIENT

Publix

3300 PUBLIX CORPORATE PARKWAY
LAKELAND, FL 33811

www.publix.com

CONSULTANT

AECOM

AECOM TECHNICAL SERVICES, INC.
800 Douglas Entrance
North Tower, 2nd Floor
Coral Gables, FL 33134
305.444.4691 tel 305.447.3580 fax
www.aecom.com

ARCHITECTURE
LICENSE NO. AA26000687

ENGINEERING
CA LIC. NO. 8115

www.aecom.com

REGISTRATION

DENNIS W. SYRJA
LICENSE
No. 43423
STATE OF FLORIDA
PROFESSIONAL ENGINEER

DENNIS W. SYRJA, P.E.
ENGINEER OF RECORD

NOTICE: THE OFFICIAL RECORD OF THIS SHEET IS THE ELECTRONIC FILE SIGNED AND SEALED UNDER RULE 61G15-23.004, F.A.C.

THIS ITEM HAS BEEN DIGITALLY SIGNED AND SEALED BY DENNIS W. SYRJA, P.E. ON THE DATE ADJACENT TO THE SEAL.

PRINTED COPIES OF THIS DOCUMENT ARE NOT CONSIDERED SIGNED AND SEALED AND THE SIGNATURE MUST BE VERIFIED ON ANY ELECTRONIC COPIES.

ISSUE/REVISION

I/R	DATE	DESCRIPTION
0	AUG 23, 2019	CONSTRUCTION DOCUMENTS

PROJECT NUMBER

60601397

SHEET TITLE

GRADING & DRAINAGE PLANS

SHEET NUMBER

CG-102

Printed on ___% Post-Consumer Recycled Content Paper
©2016 AECOM Corporation