Project Management Initials: Designer: NJR Checked: KMW Approved: DWS ARCH E1 30"x42"

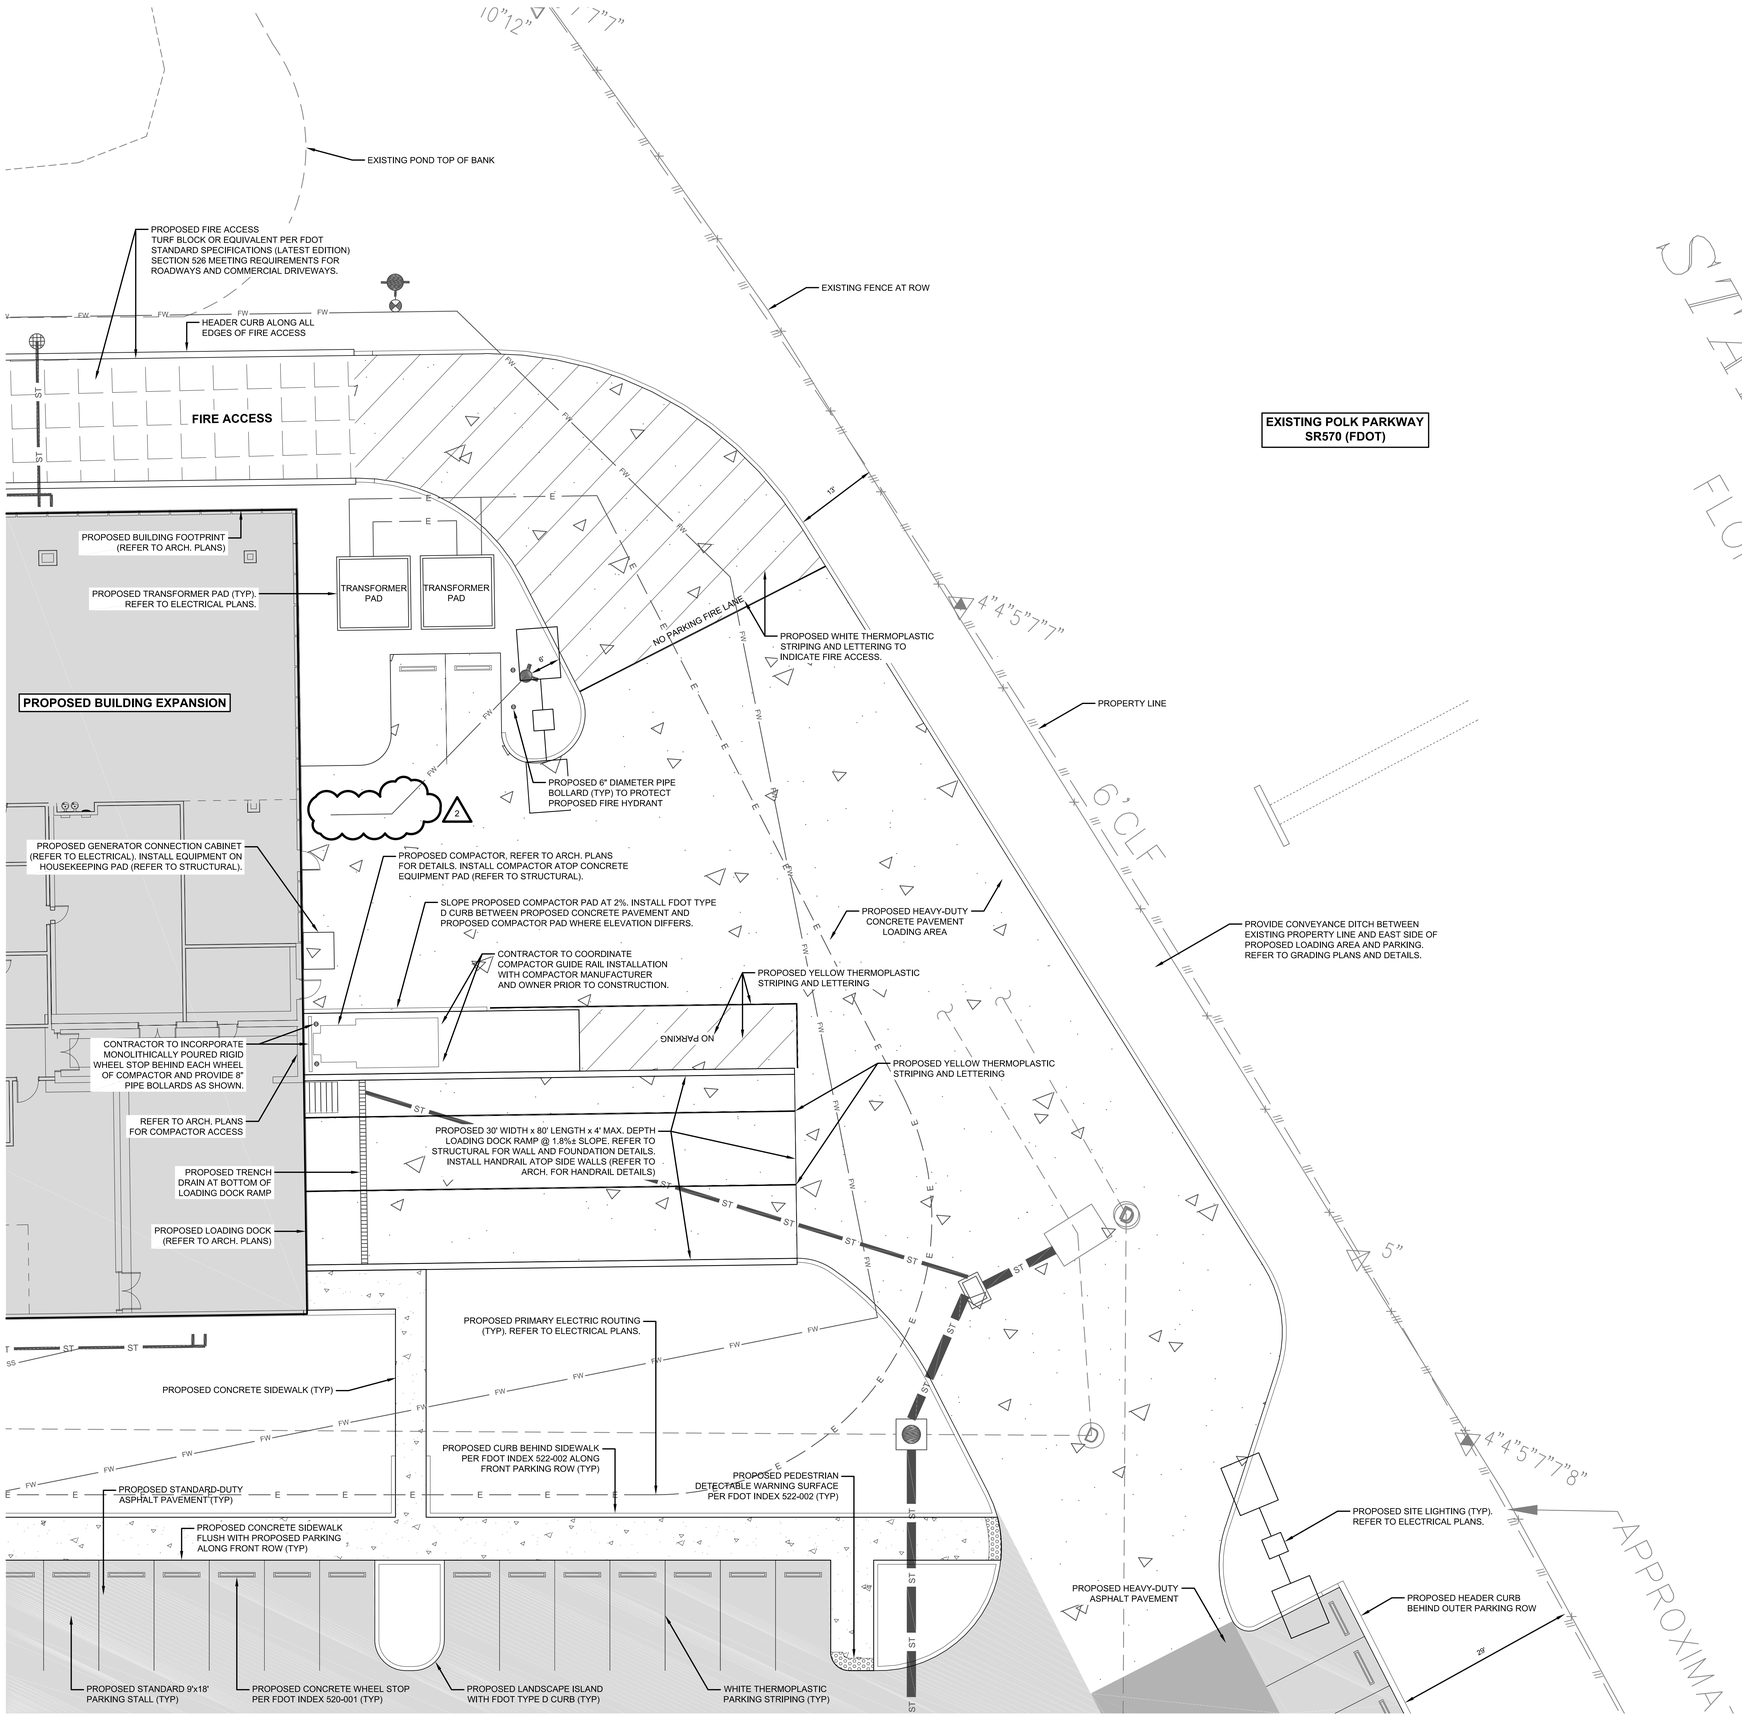

KEY MAP

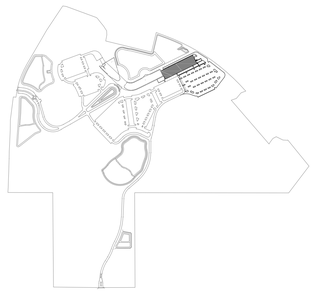

SITE / PAVING LEGEND

- PROPERTY LINE
- PROPOSED PROJECT LIMITS
- EXISTING WETLAND JURISDICTION LINE
- WETLAND SETBACK LINE
- PROPOSED HEAVY-DUTY ASPHALT PAVEMENT
- PROPOSED STANDARD-DUTY ASPHALT PAVEMENT
- PROPOSED CONCRETE PAVEMENT
- PROPOSED CONCRETE SIDEWALK
- PROPOSED TURF BLOCK OR EQUIVALENT. SEE FIRE ACCESS CALLOUT THIS SHEET.

NOTES:

- REFER TO ARCHITECTURAL, STRUCTURAL, ELECTRICAL, LIGHTING, MECHANICAL, PLUMBING, FIRE PROTECTION, AND LANDSCAPE PLANS FOR FURTHER INFORMATION AND DETAILS.
- REFER TO SHEET CS-100 FOR OVERALL SITE PLAN OF THE PUBLIX CORPORATE HEADQUARTERS FACILITY.
- REFER TO SHEET CS-101 FOR FULL PROJECT SITE AND PAVING PLAN.
- REFER TO PAVING GRADING DRAINAGE DETAILS, SHEET CG-503, FOR PROPOSED PAVEMENT SECTIONS.
- ALL PROPOSED CONCRETE SIDEWALK TO HAVE ROCK SALT FINISH UNLESS OTHERWISE NOTED. REFER TO DETAIL, SHEET CG-502.
- REFER TO SITE DETAILS, SHEET CS-501, FOR ADDITIONAL NOTES AND DETAILS.

NORTH

0 10' 20'
GRAPHIC SCALE

Building Inspection Division
Lakeland
THESE PLANS HAVE BEEN REVIEWED FOR COMPLIANCE WITH THE CURRENT EDITION. OF THE FLORIDA BUILDING CODE OR THE CITY OF LAKELAND LAND DEVELOPMENT CODE
Date: 07/16/20
Permit Number: BLD19-06035

AECOM
BATSON-COOK CONSTRUCTION

PROJECT

PUBLIX HEADQUARTERS BUILDING ADDITION AND PARKING LOT EXPANSION

3300 PUBLIX CORPORATE PARKWAY
LAKELAND, FL 33811

CLIENT

Publix
3300 PUBLIX CORPORATE PARKWAY
LAKELAND, FL 33811

www.publix.com

CONSULTANT

AECOM

AECOM TECHNICAL SERVICES, INC.
800 Douglas Entrance
North Tower, 2nd Floor
Coral Gables, FL 33134
305.444.4691 tel 305.447.3580 fax
www.aecom.com

ARCHITECTURE
LICENSE NO. AA26000687

ENGINEERING
CA LIC. NO. 8115

www.aecom.com

REGISTRATION

DENNIS W. SYRJA
LICENSE
No. 43423
STATE OF FLORIDA
PROFESSIONAL ENGINEER

DENNIS W. SYRJA, P.E.
ENGINEER OF RECORD

NOTICE: THE OFFICIAL RECORD OF THIS SHEET IS THE ELECTRONIC FILE SIGNED AND SEALED UNDER RULE 61G15-23.004, F.A.C.

THIS ITEM HAS BEEN DIGITALLY SIGNED AND SEALED BY DENNIS W. SYRJA, P.E. ON THE DATE ADJACENT TO THE SEAL.

PRINTED COPIES OF THIS DOCUMENT ARE NOT CONSIDERED SIGNED AND SEALED AND THE SIGNATURE MUST BE VERIFIED ON ANY ELECTRONIC COPIES.

ASI 5
BCC Received 5.20.2020

ISSUE/REVISION

I/R	DATE	DESCRIPTION
2	MAY 19, 2020	SI #005
1	SEP 20, 2019	100% CONSTRUCTION DOCUMENTS

PROJECT NUMBER

60601397

SHEET TITLE

ENLARGED LOADING AREA PLAN

SHEET NUMBER

CS-102

Last Plotted: 5/19/2020 5:57:03 PM
Filename: S:\PROJECTS_CIVIL\1PROJECTS\PUBLIX\600-DWG\600-CAD_BIM (CIVIL)\20-SHEETS\CCS-101 SITE PLAN.DWG
Printed on ___% Post-Consumer Recycled Content Paper
©2016 AECOM Corporation