UTILITY PLAN
ARCH E1 30"x42"

Approved: DWS
Checked: KMW
Designer: NJR
Project Management Initials:

Building Inspection Division
THESE PLANS HAVE BEEN REVIEWED FOR COMPLIANCE WITH THE CURRENT EDITION OF THE FLORIDA BUILDING CODE
Date: 11/15/19
Permit Number: BLD19-06035

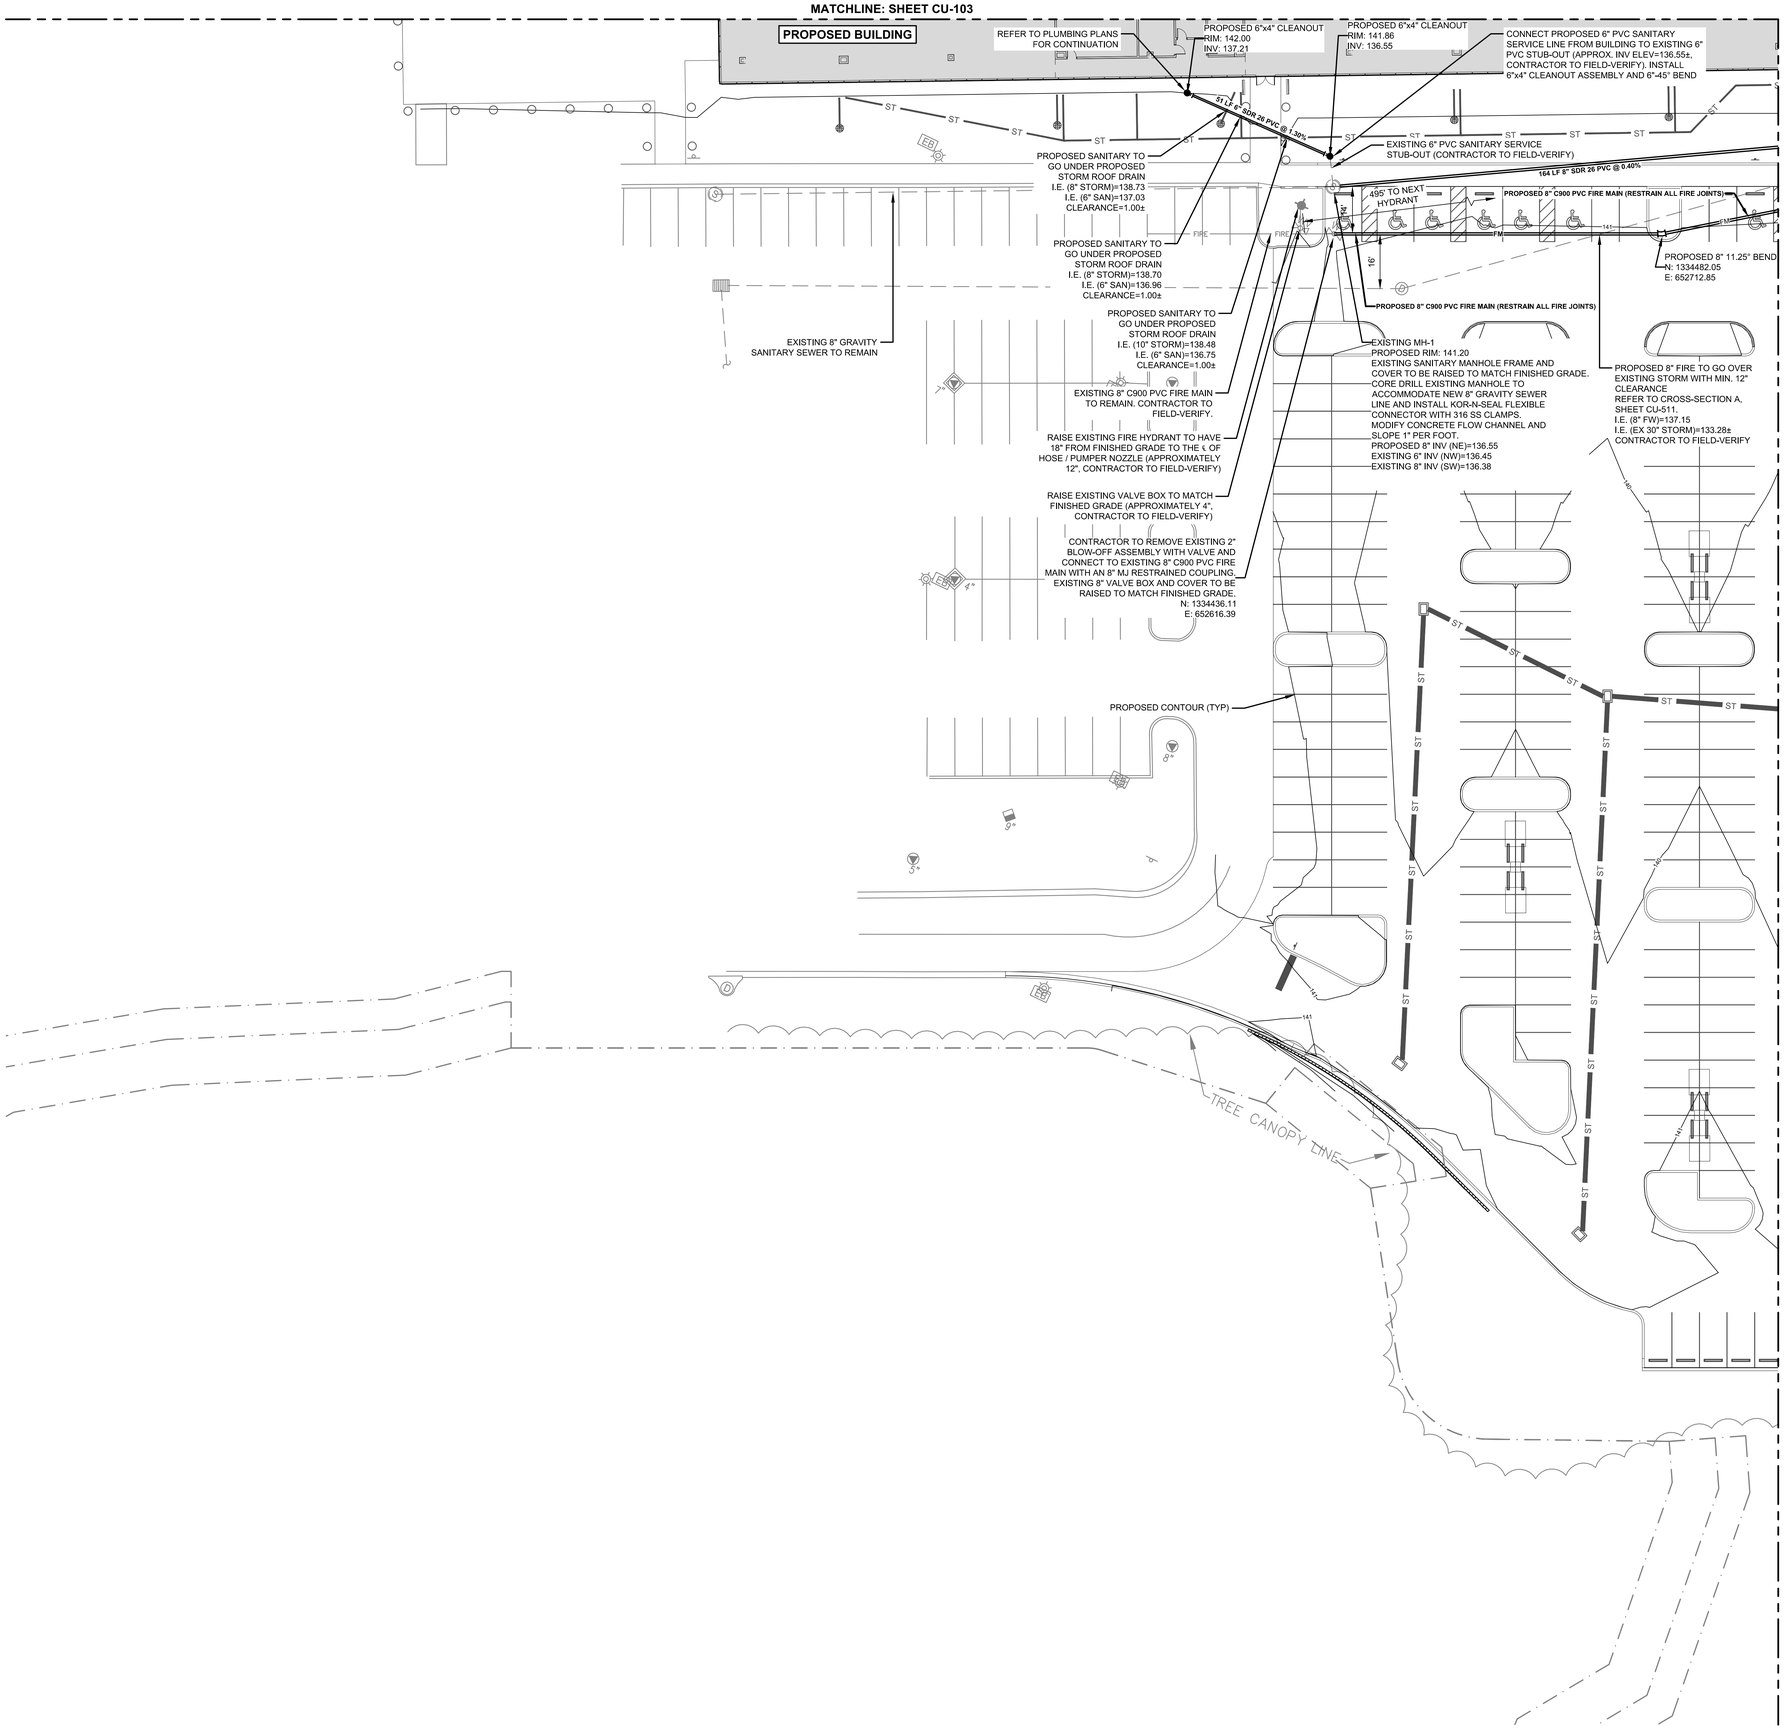

KEY MAP

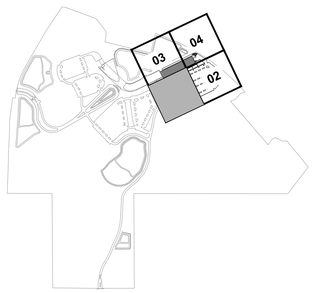

UTILITY PLAN LEGEND

FM	PROPOSED FIRE MAIN
164 LF 8" SDR 26 PVC @ 0.40%	PROPOSED SANITARY SEWER
FIRE — FIRE	EXISTING FIRE MAIN
	EXISTING SANITARY SEWER
	PROPOSED CLEANOUT
	PROPOSED REDUCER
	PROPOSED FIRE HYDRANT ASSEMBLY
	PROPOSED BEND
	PROPOSED VALVE
	PROPOSED FDC
	PROPOSED CONTOUR

NOTES:

- MAINTAIN 3FT MIN. COVER ON ALL FIRE LINE.
- REFER TO GRADING AND DRAINAGE PLANS (SHEETS CG-101 THROUGH CG-104) FOR PROPOSED STORM AND ROOF DRAIN INFORMATION AND ADDITIONAL GRADING DETAIL.
- WATER AND FIRE SERVICE TO PROPOSED NEW BUILDING ADDITION TO BE PROVIDED INTERNALLY VIA THE EXISTING BUILDING. REFER TO PLUMBING AND FIRE PROTECTION PLANS.
- REFER TO ARCHITECTURAL, MECHANICAL, AND PLUMBING DRAWINGS FOR ADDITIONAL INFORMATION ON PROPOSED ROOF DRAIN AND UTILITY CONNECTION LOCATIONS AND DETAILS.
- VERTICAL DATUM: NORTH AMERICAN VERTICAL DATUM 1988 (NAVD88). ALL EXISTING AND PROPOSED ELEVATIONS DEPICTED ARE IN FEET NAVD88 (UNLESS OTHERWISE NOTED). TO OBTAIN NATIONAL GEODETIC VERTICAL DATUM 1929 (NGVD29), ADD 0.85 FT TO ELEVATIONS IN NAVD88.
- REFER TO UTILITY DETAILS, SHEETS CU-501 THROUGH CU-502.
- EXISTING UTILITY AND STORM INFORMATION ARE APPROXIMATE. CONTRACTOR IS RESPONSIBLE FOR FIELD VERIFYING ALL EXISTING CONDITIONS PRIOR TO CONSTRUCTION.
- ALL WORK SHALL BE PERFORMED TO CURRENT CITY OF LAKELAND STANDARDS AND SPECIFICATIONS.
- ALL PROPOSED UTILITIES DEPICTED ARE PRIVATE.

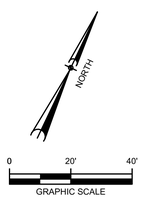

AECOM
BATSON-COOK CONSTRUCTION

PROJECT

PUBLIX HEADQUARTERS BUILDING ADDITION AND PARKING LOT EXPANSION

3300 PUBLIX CORPORATE PARKWAY
LAKELAND, FL 33811

CLIENT

Publix

3300 PUBLIX CORPORATE PARKWAY
LAKELAND, FL 33811

www.publix.com

CONSULTANT

AECOM

AECOM TECHNICAL SERVICES, INC.
800 Douglas Entrance
North Tower, 2nd Floor
Coral Gables, FL 33134
305.444.4691 tel 305.447.3580 fax
www.aecom.com

ARCHITECTURE
LICENSE NO. AA26000687

ENGINEERING
CA LIC. NO. 8115

www.aecom.com

Digitally signed by Dennis W Syrja
Date: 2019.08.23 10:46:14 -04'00'

REGISTRATION

DENNIS W. SYRJA
LICENSE
No. 43423
STATE OF FLORIDA
PROFESSIONAL ENGINEER

DENNIS W. SYRJA, P.E.
ENGINEER OF RECORD

NOTICE: THE OFFICIAL RECORD OF THIS SHEET IS THE ELECTRONIC FILE SIGNED AND SEALED UNDER RULE 61G15-23.004, F.A.C.

THIS ITEM HAS BEEN DIGITALLY SIGNED AND SEALED BY DENNIS W. SYRJA, P.E. ON THE DATE ADJACENT TO THE SEAL.

PRINTED COPIES OF THIS DOCUMENT ARE NOT CONSIDERED SIGNED AND SEALED AND THE SIGNATURE MUST BE VERIFIED ON ANY ELECTRONIC COPIES.

ISSUE/REVISION

I/R	DATE	DESCRIPTION
0	AUG 23, 2019	CONSTRUCTION DOCUMENTS

PROJECT NUMBER

60601397

SHEET TITLE

UTILITY PLAN

SHEET NUMBER

CU-101

©2016 AECOM Corporation

Last Plotted: 8/22/2019 8:29:55 PM
Filename: S:\PROJECTS_CIVIL\PROJECTS\PUBLIX\600-DWG\600-CAD_BIM (CIVIL)\20-SHEETS\CCU-101 UTILITY PLAN.DWG

Printed on ___% Post-Consumer Recycled Content Paper