E1-1-00-OVERALL ELECTRICAL SITE PLAN
Project Management Initials: Designer: Designer Checker: Checker Approved: Approver/RCH E1 30"x42"

GENERAL NOTES:
1. EC SHALL PROVIDE AND INSTALL PRIMARY CONDUITS ORIGINATING FROM EXISTING LAKELAND ELECTRIC MANHOLE AND TERMINATING INTO TRANSFORMER LOCATIONS
2. REFER TO LAKELAND ELECTRIC'S POLICIES AND SPECIFICATIONS FOR SUBDIVISOON AND COMMERCIAL DEVELOPMENTS FOR ALL REQUIREMENTS ASSOCIATED WITH THE INSTALLATION OF THE PRIMARY FEEDERS.
3. PULLBOXES SHALL BE A MINIMUM 4'X6'.
4. ALL PRIMARY CONDUITS SHALL BE 4" CONDUIT CONCRETE ENCASED.
5. PRIMARY FEEDER CIRCUITS ARE SHOWN FOR REFERENCE AND BIDDING PURPOSES ONLY. COORDINATE CONDUIT ROUTING WITH LAKELAND ELECTRIC DESIGN DRAWINGS PRIOR TO ROUGH-IN.
6. ALL PRIMARY ELBOW SWEEPS SHALL BE ALUMINUM
7. CONTRACTOR SHALL PROVIDE AND INSTALL TRANSFORMER PADS AS SPECIFIED IN DRAWING
8. CONTRACTOR SHALL PROVIDE AND INSTALL CONCRETE PRIMARY METERING CABINET PADS AS SPECIFIED.
9. CONTRACTOR SHALL PROVIED AND INSTALL MANHOLES AS SPECIFIED
10. LAKELAND ELECTRIC WILL NOT ENERGIZE SERVICE UNTIL ALL DOCUMENTS REQUIRED BY LAKELAND ELECTRIC HAVE BEEN PROPERLY SIGNED AND ORIGINALS RETURNED TO LAKELAND ELECTRIC AS SPECIFIED BY LAKELAND ELECTRIC'S COMMERCIAL DEVELOPMENT POLICY FOR INDIVIDUAL COMMERCIAL PROJECTS.
11. UNDER NO CIRCUMSTANCE SHALL ANY POLICY, STANDARD OR SPECIFICATION OF LAKELAND ELECTRIC'S BE DEVIATED FROM UNLESS PRIOR WRITTEN APPROVAL HAS BEEN OBTAINED FROM LAKELAND ELECTRIC.
12. LAKELAND ELECTRIC CONTACT JAY ELLIS AT 863-834-8868

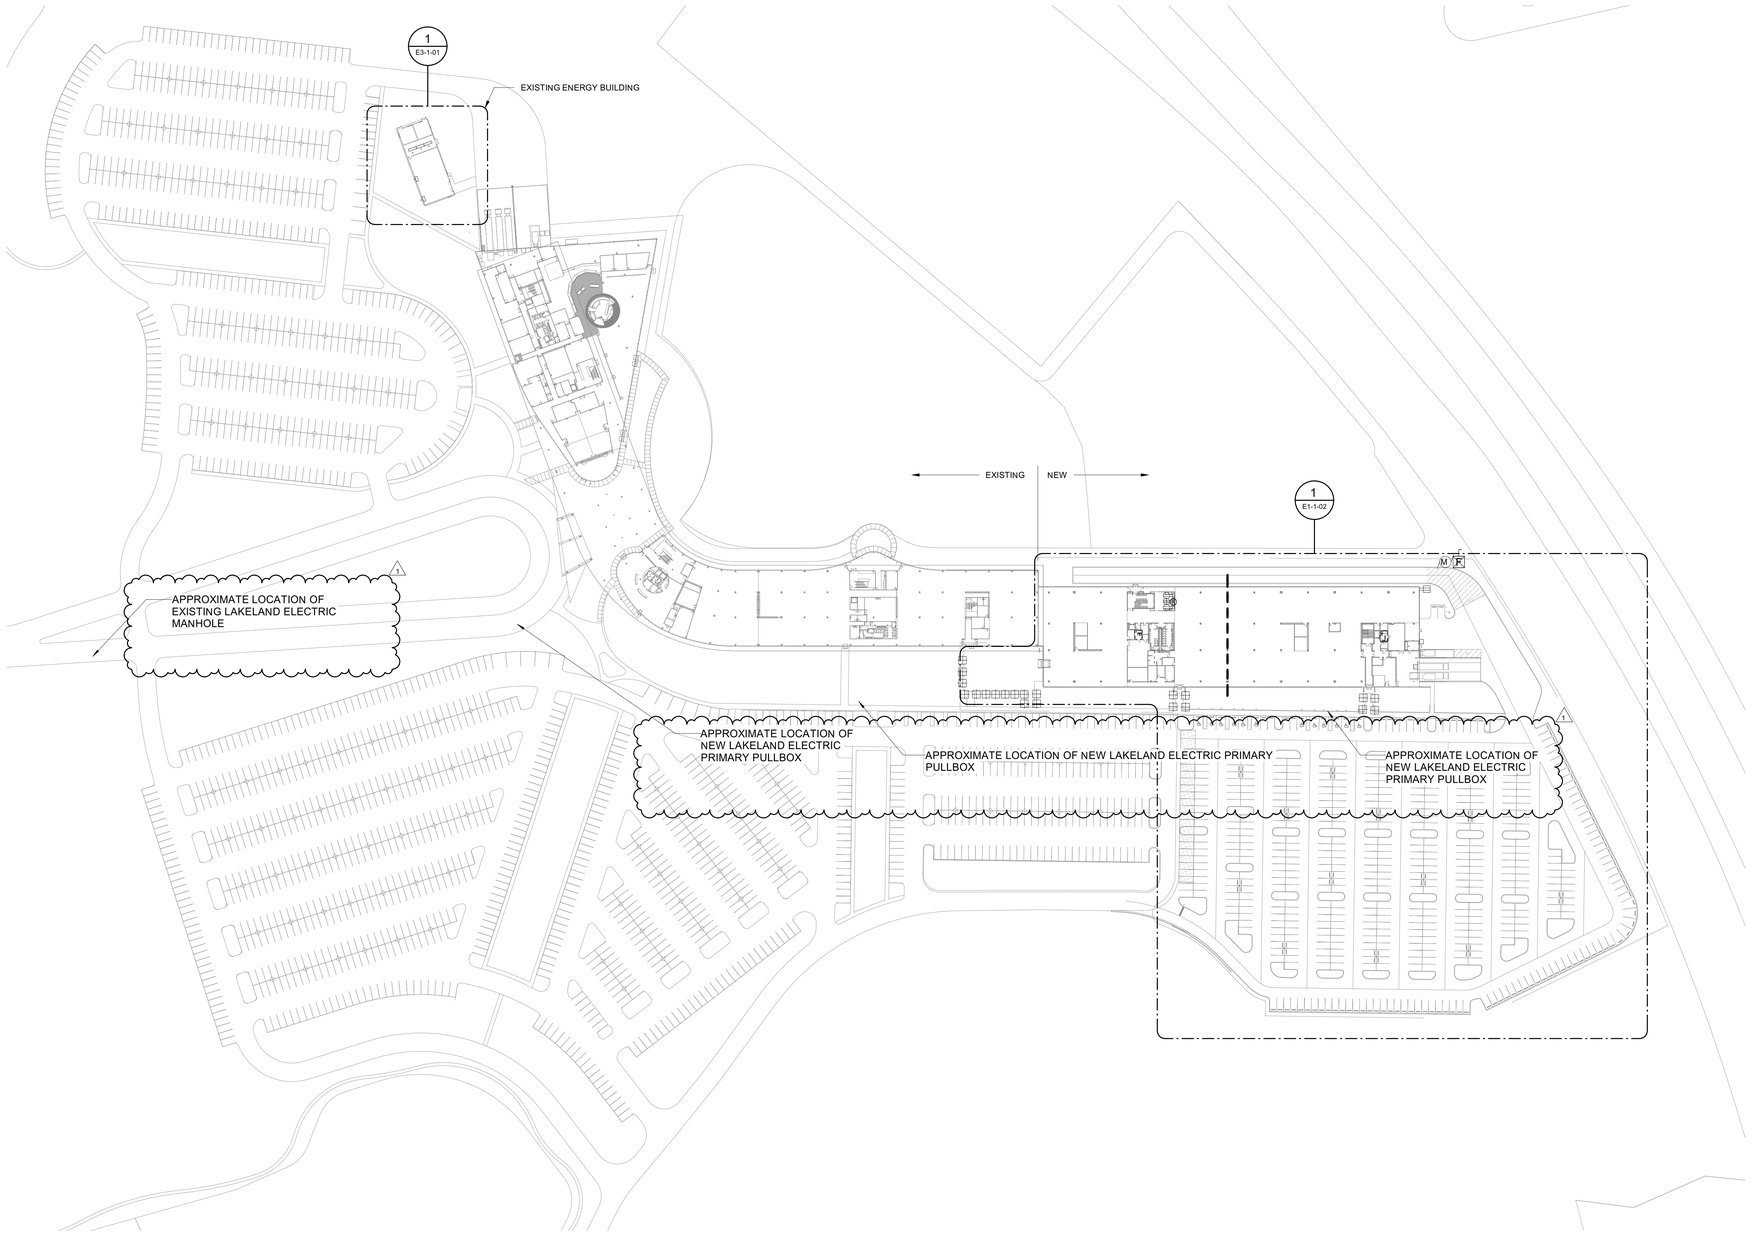

1 **OVERALL ELECTRICAL SITE PLAN**
Scale: 1" = 80'-0"
SCALE: 1" = 40'-0" 0 20' 40' 80' 120'

N TN

Last Plotted: 9/30/2019 5:01:32 PM
Filename: BIM 360/60601397-Publix HQ/60601397_Publix HQ_ELECT_R2019.rvt

Printed on ___% Post-Consumer Recycled Content Paper

©2016 AECOM Corporation

Building Inspection Division
Lakeland
THESE PLANS HAVE BEEN REVIEWED FOR COMPLIANCE WITH THE CURRENT EDITION OF THE FLORIDA BUILDING CODE
Date: 11/15/19
Permit Number: BLD19-06035

AECOM
BATSON-COOK CONSTRUCTION

PROJECT

PUBLIX HEADQUARTERS BUILDING ADDITION AND PARKING LOT EXPANSION

3300 PUBLIX CORPORATE PARKWAY
LAKELAND, FL 33811

CLIENT

Publix

3300 PUBLIX CORPORATE PARKWAY
LAKELAND, FL 33811

www.publix.com

CONSULTANT

AECOM

AECOM TECHNICAL SERVICES, INC.
800 Douglas Entrance
North Tower, 2nd Floor
Coral Gables, FL 33134
305.444.4691 tel 305.447.3580 fax
www.aecom.com

ARCHITECTURE
LICENSE NO. AA26000687

ENGINEERING
CA LIC. NO. 8115

http://www.aecom.com

REGISTRATION

HENRYK B. JUSZCZYK LICENSE NO. 58082 STATE OF FLORIDA PROFESSIONAL ENGINEER

HENRYK B. JUSZCZYK, PROFESSIONAL ENGINEER, STATE OF FLORIDA, LICENSE NO. 58082

THIS ITEM HAS BEEN DIGITALLY SIGNED AND SEALED BY HENRYK B. JUSZCZYK, PROFESSIONAL ENGINEER, STATE OF FLORIDA, LICENSE NO. 58082 ON THE DATE INDICATED HERE. PRINTED COPIES OF THIS DOCUMENT ARE NOT CONSIDERED SIGNED AND SEALED AND THE SIGNATURE MUST BE VERIFIED ON ANY ELECTRONIC COPIES.

Henryk B Juszczyk
2019.09.30 18:00:20
-04'00'

KEY PLAN

EXISTING	A	B

ISSUE/REVISION

I/R	DATE	DESCRIPTION
1	SEP 30, 2019	100% CONSTRUCTION DOCUMENTS
0	AUG 23, 2019	CONSTRUCTION DOCUMENTS

PROJECT NUMBER

60601397

SHEET TITLE

OVERALL ELECTRICAL SITE PLAN

SHEET NUMBER

E1-1-00

NOTICE: THE OFFICIAL RECORD OF THIS SHEET IS THE ELECTRONIC FILE SIGNED AND SEALED UNDER RULE 61G15-23.004, F.A.C.