ELECTRICAL SITE PLAN - PHOTOMETRICS
Project Management Initials: Designer: MJR Checked: KMW Approved: DWS ARCH E1 30"x42"

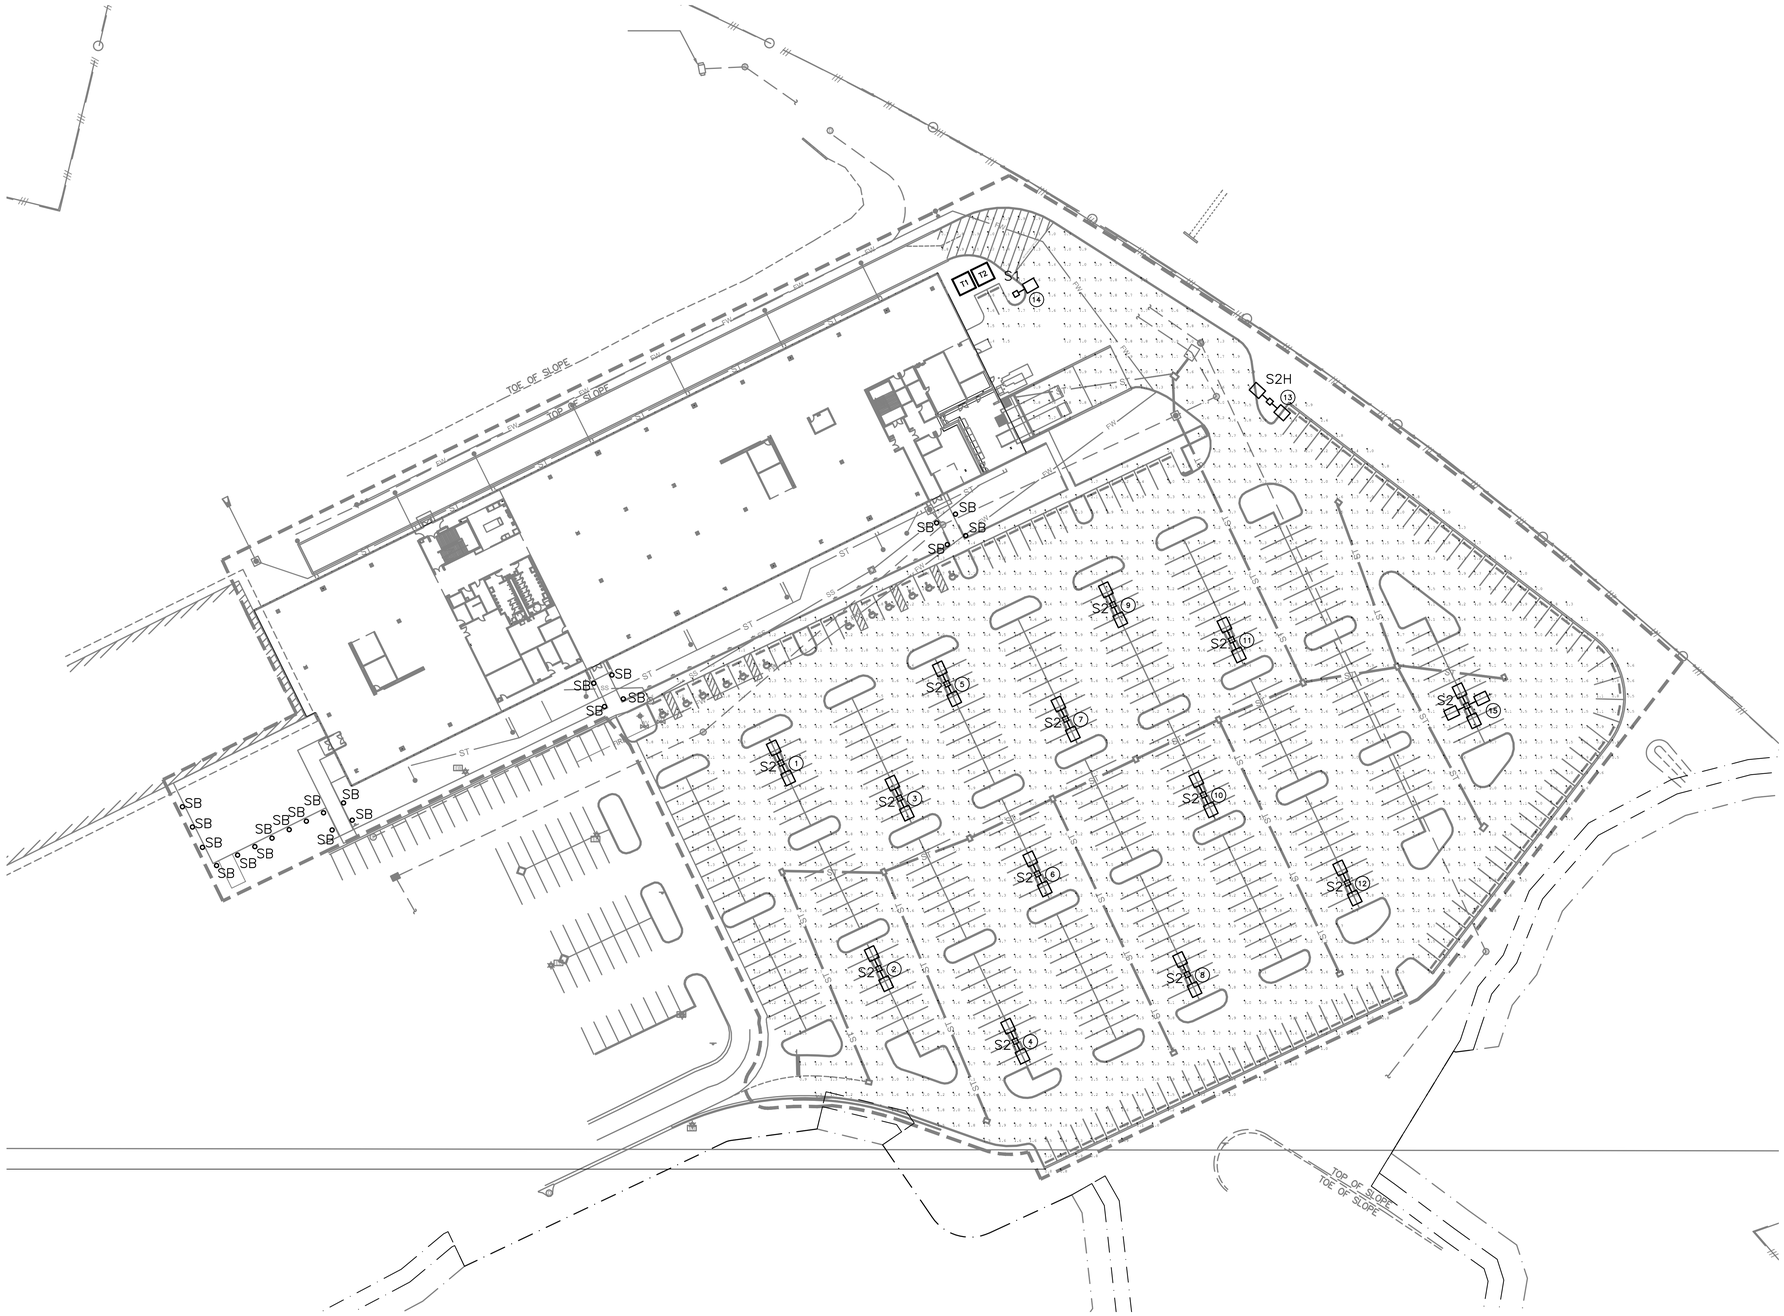

Luminaire Schedule							
Symbol	Label	Arrangement	Lumens / Fixture	VOLT	LLF	Description	
	S1 - 30 FOOT MOUNTING HEIGHT	SINGLE	31,000	480	0.880	RSX2 LED P6 40K R5	
	S2 - 30 FOOT MOUNTING HEIGHT	BACK-BACK	31,000	480	0.880	RSX2 LED P6 40K R5	
	S4 - 30 FOOT MOUNTING HEIGHT	4 @ 90 DEGREES	31,000	480	0.880	RSX2 LED P6 40K R5	
	S2H - 30 FOOT MOUNTING HEIGHT	TWIN	21,000	480	0.880	RSX2 LED P6 40K R5 EGS	
	SB - BOLLARD	SINGLE	21,000	277	0.880	DSBX LED 16C 450 40K SYM	

Calculation Summary							
Label	CalcType	Units	Avg	Max	Min	Avg/Min	Max/Min
PARKING AREA	Illuminance	Fc	3.56	7.1	0.5	7.12	14.20
TRUCK DOCK AREA	Illuminance	Fc	1.22	3.3	0.5	2.44	6.60

ELECTRICAL SYMBOL LEGEND:

S #	LED POLE MOUNTED SITE LIGHTING FIXTURE. LETTER INDICATES FIXTURE TYPE. SEE LIGHTING FIXTURE SCHEDULE. PROVIDE QUANTITIES AS SHOWN ON DRAWINGS AND INDICATED IN FIXTURE SCHEDULE. # INDICATES POLE NUMBER.
SB	LED GROUND MOUNTED BOLLARD LIGHTING FIXTURE. LETTER INDICATES FIXTURE TYPE. SEE LIGHTING FIXTURE SCHEDULE. PROVIDE QUANTITIES AS SHOWN ON DRAWINGS.

NOTES:

1. **PHOTOMETRIC CALCULATIONS WERE PRODUCED WITH AGI32 VERSION 17.4 WITH ACUITY BRAND LITHONIA RSX2 SERIES AREA LIGHTING.**

NORTH

0 40' 80'
GRAPHIC SCALE

Building Inspection Division
THESE PLANS HAVE BEEN REVIEWED FOR COMPLIANCE WITH THE CURRENT EDITION OF THE FLORIDA BUILDING CODE
Lakeland
Date: 11/15/19
Permit Number: BLD19-06035

AECOM
BATSON-COOK CONSTRUCTION

PROJECT

PUBLIX HEADQUARTERS BUILDING ADDITION AND PARKING LOT EXPANSION

3300 PUBLIX CORPORATE PARKWAY
LAKELAND, FL 33811

CLIENT

Publix

3300 PUBLIX CORPORATE PARKWAY
LAKELAND, FL 33811

www.publix.com

CONSULTANT

AECOM

AECOM TECHNICAL SERVICES, INC.
800 Douglas Entrance
North Tower, 2nd Floor
Coral Gables, FL 33134
305.444.4691 tel 305.447.3580 fax
www.aecom.com

ARCHITECTURE
LICENSE NO. AA26000687

ENGINEERING
CA LIC. NO. 8115

www.aecom.com

REGISTRATION

HENRYK B. JUSZCZYK LICENSE No 58082 STATE OF FLORIDA PROFESSIONAL ENGINEER

ENGINEER OF RECORD
Henryk B. Juszczyk P.E. No. 58082

NOTICE: THE OFFICIAL RECORD OF THIS SHEET IS THE ELECTRONIC FILE SIGNED AND SEALED UNDER RULE 61G15-23.004, F.A.C.

THIS ITEM HAS BEEN DIGITALLY SIGNED AND SEALED BY HENRYK B. JUSZCZYK, P.E. ON THE DATE ADJACENT TO THE SEAL.

PRINTED COPIES OF THIS DOCUMENT ARE NOT CONSIDERED SIGNED AND SEALED AND THE SIGNATURE MUST BE VERIFIED ON ANY ELECTRONIC COPIES.

Henryk B Juszczyk
2019.08.22
22:57:44 -04'00'

ISSUE/REVISION

I/R	DATE	DESCRIPTION
0	AUG 23, 2019	CONSTRUCTION DOCUMENTS

PROJECT NUMBER

60601397

SHEET TITLE

ELECTRICAL SITE PLAN - PHOTOMETRICS

SHEET NUMBER

E1-1-01

Last Plotted: 8/22/2019 1:35:45 PM
Filename: \\US\CQB1PP\P0001\NEW\PROJECTS\60601397 PUBLIX CORPORATE HQ EXPANSION\900-WORK\10-CAD_BIM\20-SHEETS\E\20-SHEETS\E1-1-01 ELECTRICAL SITE PLAN.DWG

Printed on ___% Post-Consumer Recycled Content Paper

©2016 AECOM Corporation