E2-2-40-OVERALL ELECTRICAL PLAN - ROOF LEVEL
Project Management Initials: Designer: Designer Checker: Checker Approved: ApproverARCH E1 30"x42"

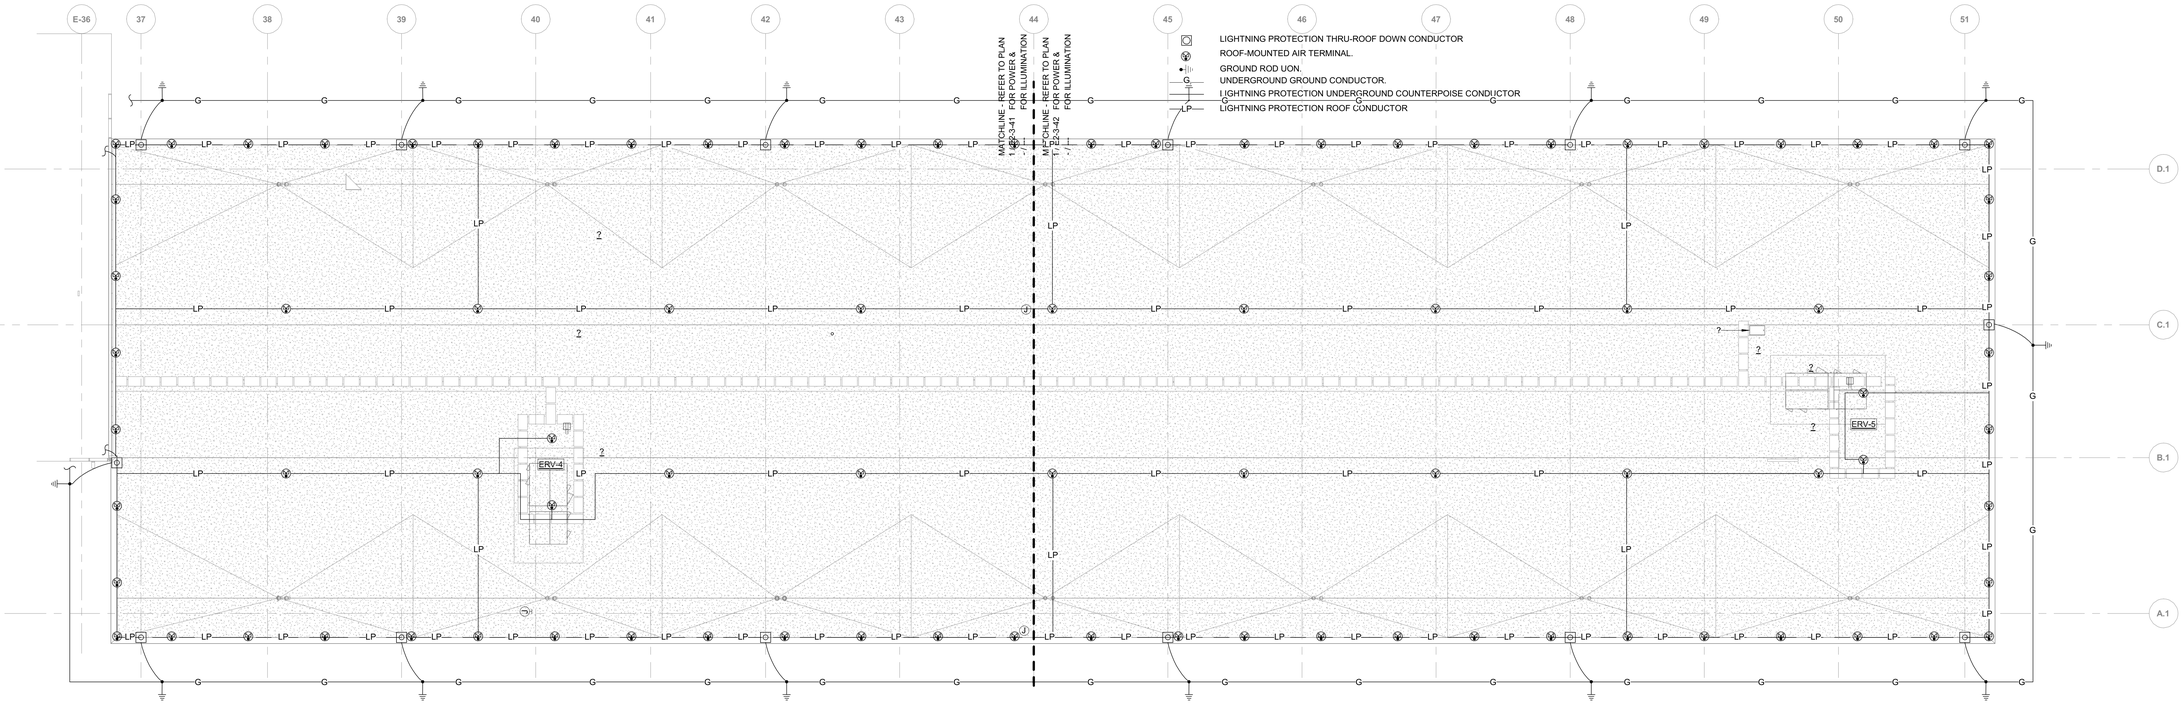

GENERAL NOTES:
1. LIGHTNING PROTECTION SYSTEM SHALL COMPLY WITH NFPA 780.
2. ALL METAL EQUIPMENT ON ROOF SHALL BE PROTECTED AND CONNECTED TO THE LIGHTNING PROTECTION SYSTEM WITH AT LEAST TWO PATHS.
3. REFER TO ENLARGED PLANS FOR ADDITIONAL INFORMATION.
4. PROVIDE UL MASTER LABEL CERTIFIED LIGHTNING PROTECTION SYSTEM. 1

1 OVERALL ELECTRICAL PLAN - LEVEL 4
Scale: 1/16" = 1'-0"

SCALE: 1/16" = 1'-0" 0 4' 8' 16' 32' 48'

N TN

Last Plotted: 9/30/2019 5:03:48 PM
Filename: BR-300-60601397-Publix HQ\60601397_Publix HQ_ELECT_R2019.rvt

Printed on ___% Post-Consumer Recycled Content Paper

©2016 AECOM Corporation

Building Inspection Division
Lakeland
THESE PLANS HAVE BEEN REVIEWED FOR COMPLIANCE WITH THE CURRENT EDITION OF THE FLORIDA BUILDING CODE
Date: 11/15/19
Permit Number: BLD19-06035

AECOM
BATSON-COOK CONSTRUCTION

PROJECT

PUBLIX HEADQUARTERS BUILDING ADDITION AND PARKING LOT EXPANSION

3300 PUBLIX CORPORATE PARKWAY
LAKELAND, FL 33811

CLIENT

Publix

3300 PUBLIX CORPORATE PARKWAY
LAKELAND, FL 33811

www.publix.com

CONSULTANT

AECOM

AECOM TECHNICAL SERVICES, INC.
800 Douglas Entrance
North Tower, 2nd Floor
Coral Gables, FL 33134
305.444.4691 tel 305.447.3580 fax
www.aecom.com

ARCHITECTURE
LICENSE NO. AA26000687

ENGINEERING
CA LIC. NO. 8115

http://www.aecom.com

REGISTRATION

HENRYK B. JUSZCZYK
LICENSE NO. 58082
STATE OF FLORIDA
PROFESSIONAL ENGINEER

HENRYK B. JUSZCZYK, PROFESSIONAL ENGINEER, STATE OF FLORIDA, LICENSE NO. 58082

THIS ITEM HAS BEEN DIGITALLY SIGNED AND SEALED BY HENRYK B. JUSZCZYK, PROFESSIONAL ENGINEER, STATE OF FLORIDA, LICENSE NO. 58082 ON THE DATE INDICATED HERE. PRINTED COPIES OF THIS DOCUMENT ARE NOT CONSIDERED SIGNED AND SEALED AND THE SIGNATURE MUST BE VERIFIED ON ANY ELECTRONIC COPIES.

Henryk B Juszczyk
2019.09.30
18:06:41 -04'00'

KEY PLAN

EXISTING | A | B

ISSUE/REVISION

I/R	DATE	DESCRIPTION
1	SEP 30, 2019	100% CONSTRUCTION DOCUMENTS
0	AUG 23, 2019	CONSTRUCTION DOCUMENTS

PROJECT NUMBER

60601397

SHEET TITLE

OVERALL ELECTRICAL PLAN - ROOF LEVEL

SHEET NUMBER

E2-2-40

NOTICE: THE OFFICIAL RECORD OF THIS SHEET IS THE ELECTRONIC FILE SIGNED AND SEALED UNDER RULE 61G15-23.004, F.A.C.