E3-1-02-ENLARGED ELECTRICAL ROOMS
Project Management Initials: Designer: Designer Checker: Checker Approved: Approver/ARCH E1 30"x42"

Building Inspection Division
Lakeland
THESE PLANS HAVE BEEN REVIEWED FOR COMPLIANCE WITH THE CURRENT EDITION OF THE FLORIDA BUILDING CODE
Date: 11/15/19
Permit Number: BLD19-06035

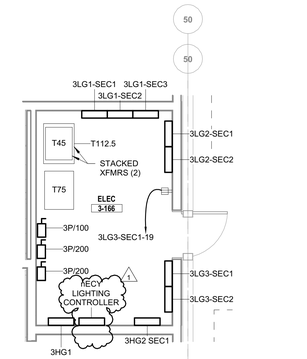

7 LEVEL 3 ELECTRICAL ROOM 3-137 - ENLARGED VIEW
Scale: 1/4" = 1'-0"

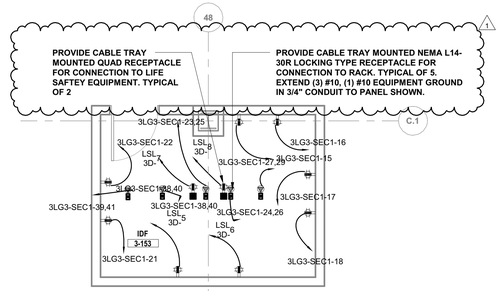

8 LEVEL 3 IDF ROOM 3-153 - ENLARGED VIEW
Scale: 1/4" = 1'-0"

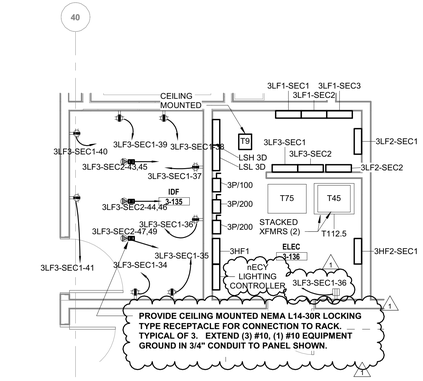

6 LEVEL 3 ELECTRICAL ROOM 3-113 & TELECOM ROOM 3-112 - ENLARGED VIEW
Scale: 1/4" = 1'-0"

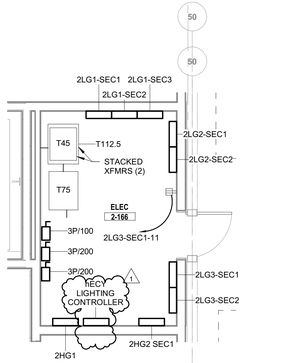

5 LEVEL 2 ELECTRICAL ROOM 2-137 - ENLARGED VIEW
Scale: 1/4" = 1'-0"

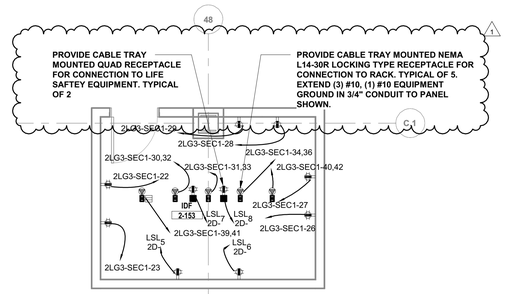

9 LEVEL 2 IDF ROOM 2-153 - ENLARGED VIEW
Scale: 1/4" = 1'-0"

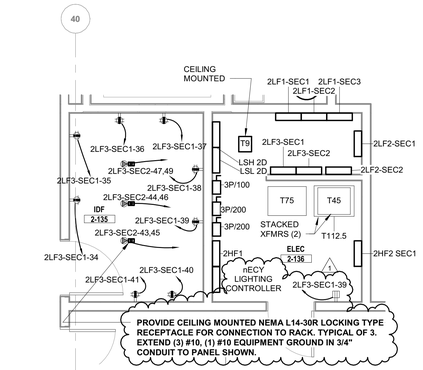

4 LEVEL 2 ELECTRICAL ROOM 2-113 & TELECOM ROOM 2-112 - ENLARGED VIEW
Scale: 1/4" = 1'-0"

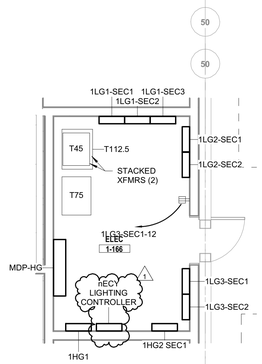

3 LEVEL 1 ELECTRICAL ROOM 1-137 - ENLARGED VIEW
Scale: 1/4" = 1'-0"

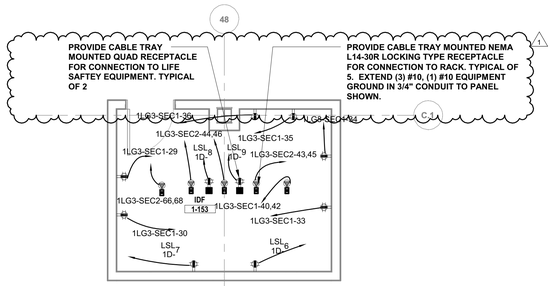

10 LEVEL 1 IDF ROOM 1-153 - ENLARGED VIEW
Scale: 1/4" = 1'-0"

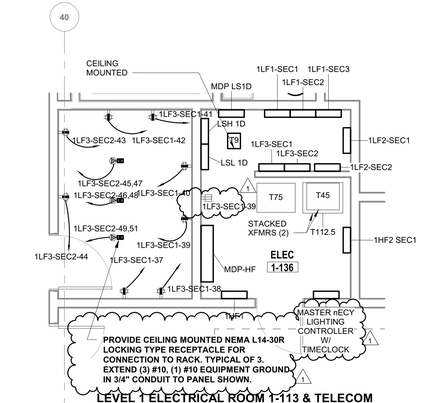

2 LEVEL 1 ELECTRICAL ROOM 1-113 & TELECOM ROOM 1-112 - ENLARGED VIEW
Scale: 1/4" = 1'-0"

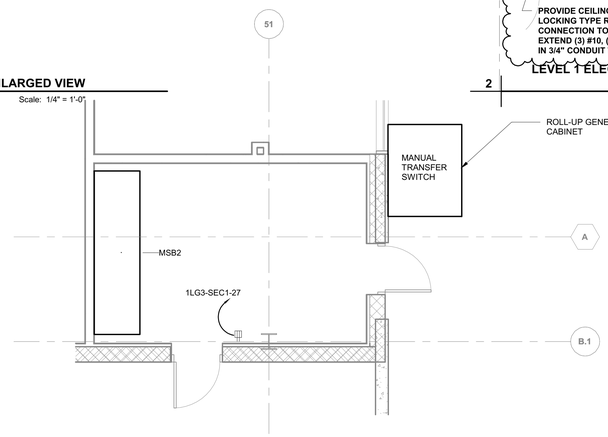

1 LEVEL 1 MAIN ELECTRICAL ELECTRICAL ROOM 1-143 - ENLARGED VIEW
Scale: 1/4" = 1'-0"

GENERAL NOTES:

1. PROVIDE (2) 3/4"X4'X8' PLYWOOD TELEPHONE BOARD IN EACH IDF ROOM. PAINT PLYWOOD WITH TWO COATS OF FIRE RETARDENT PAINT.
2. CEILING MOUNTED RECEPTACLES IN IDF ROOMS SHALL BE COORDINATED WITH THE VENDORS FOR LOCATION, REQUIRMENTS, AND QUANTITY.

SCALE: 1/4" = 1'-0" 0 1' 2' 4' 8' 12'

N TN

AECOM
BATSON-COOK CONSTRUCTION

PROJECT

PUBLIX HEADQUARTERS BUILDING ADDITION AND PARKING LOT EXPANSION

3300 PUBLIX CORPORATE PARKWAY
LAKELAND, FL 33811

CLIENT

Publix

3300 PUBLIX CORPORATE PARKWAY
LAKELAND, FL 33811

www.publix.com

CONSULTANT

AECOM

AECOM TECHNICAL SERVICES, INC.
800 Douglas Entrance
North Tower, 2nd Floor
Coral Gables, FL 33134
305.444.4691 tel 305.447.3580 fax
www.aecom.com

ARCHITECTURE
LICENSE NO. AA26000687

ENGINEERING
CA LIC. NO. 8115

http://www.aecom.com

REGISTRATION

HENRYK B. JUSZCZYK LICENSE NO. 58082 STATE OF FLORIDA PROFESSIONAL ENGINEER

HENRYK B. JUSZCZYK, PROFESSIONAL ENGINEER, STATE OF FLORIDA, LICENSE NO. 58082

THIS ITEM HAS BEEN DIGITALLY SIGNED AND SEALED BY HENRYK B. JUSZCZYK, PROFESSIONAL ENGINEER, STATE OF FLORIDA, LICENSE NO. 58082 ON THE DATE INDICATED HERE. PRINTED COPIES OF THIS DOCUMENT ARE NOT CONSIDERED SIGNED AND SEALED AND THE SIGNATURE MUST BE VERIFIED ON ANY ELECTRONIC COPIES.

Henryk B Juszczyk
2019.09.30
18:08:49 -04'00'

NOTICE: THE OFFICIAL RECORD OF THIS SHEET IS THE ELECTRONIC FILE SIGNED AND SEALED UNDER RULE 61G15-23.004, F.A.C.

ISSUE/REVISION

I/R	DATE	DESCRIPTION
1	SEP 30, 2019	100% CONSTRUCTION DOCUMENTS
0	AUG 23, 2019	CONSTRUCTION DOCUMENTS

PROJECT NUMBER

60601397

SHEET TITLE

ENLARGED ELECTRICAL ROOMS

SHEET NUMBER

E3-1-02

Last Plotted: 9/30/2019 5:04:44 PM
Filename: BM_60601397_Publix HQ\60601397_Publix HQ_ELECT_R2019.rvt

Printed on ___% Post-Consumer Recycled Content Paper

©2016 AECOM Corporation