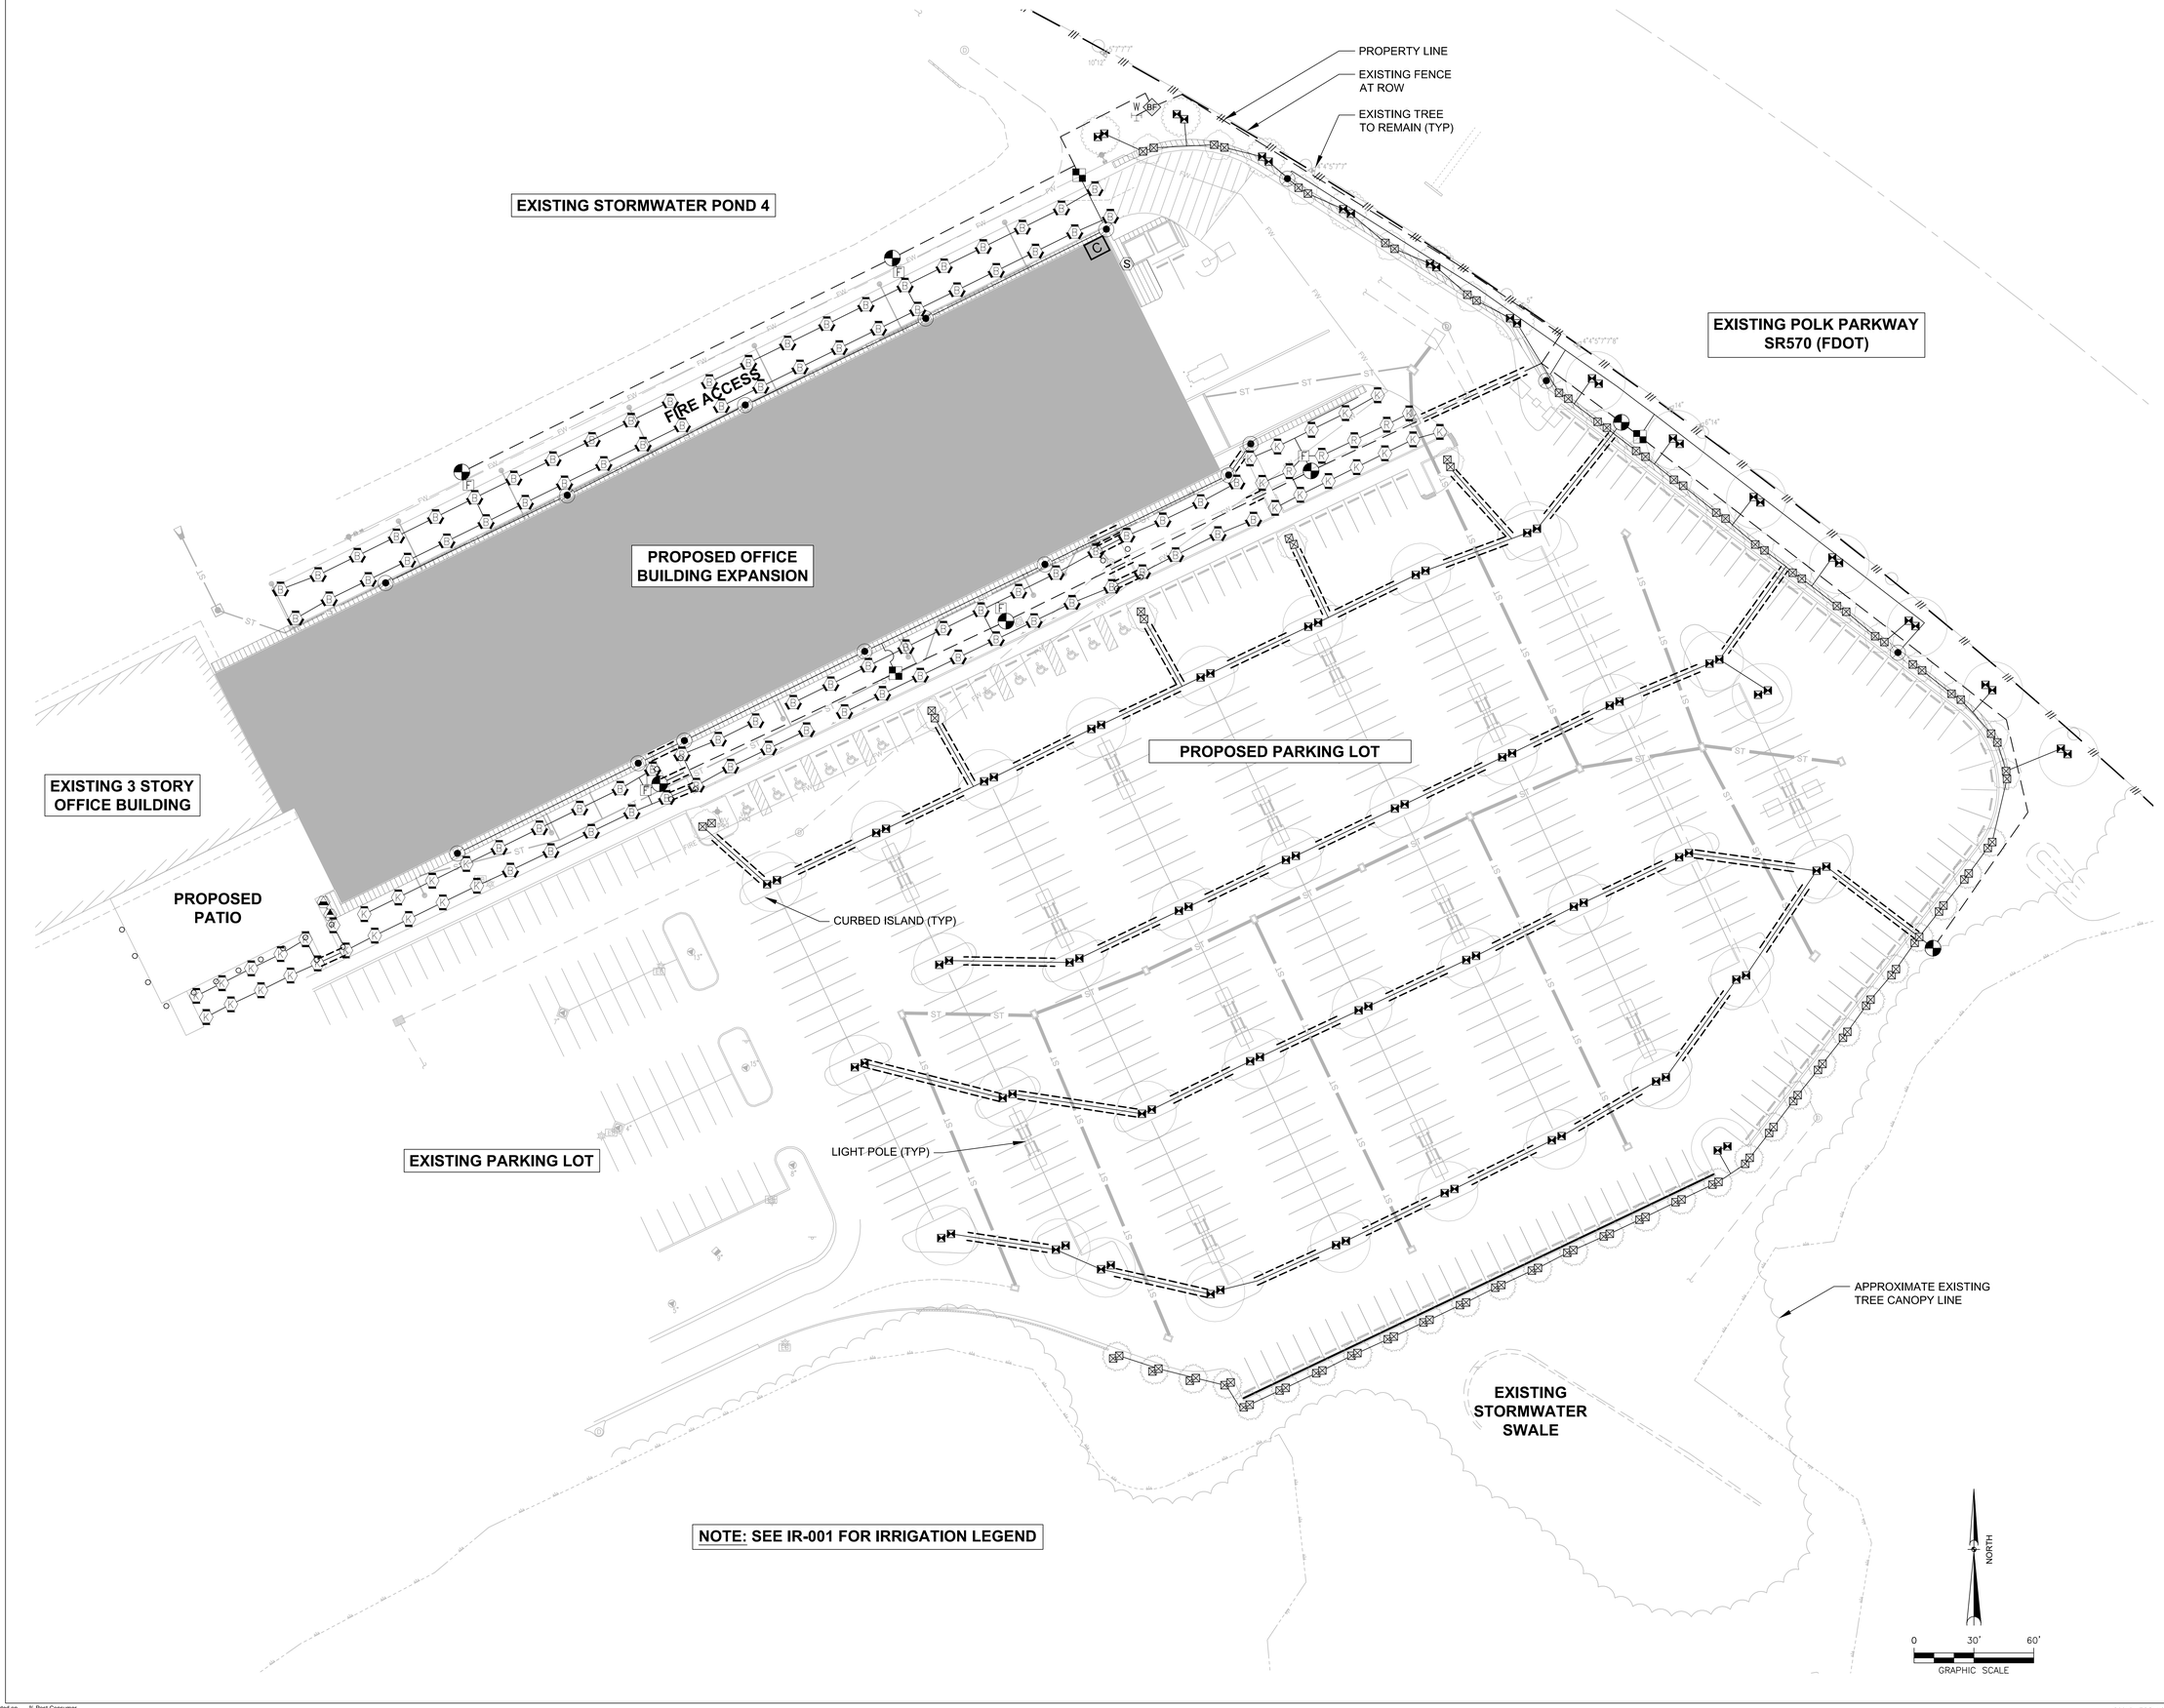

NOTE: SEE IR-001 FOR IRRIGATION LEGEND

Building Inspection Division
THESE PLANS HAVE BEEN REVIEWED FOR COMPLIANCE WITH THE CURRENT EDITION OF THE FLORIDA BUILDING CODE
Date: 11/15/19
Permit Number: BLD19-06035

AECOM
BATSON-COOK CONSTRUCTION

PROJECT

PUBLIX HEADQUARTERS BUILDING ADDITION AND PARKING LOT EXPANSION

3300 PUBLIX CORPORATE PARKWAY
LAKELAND, FL 33811

CLIENT

Publix

3300 PUBLIX CORPORATE PARKWAY
LAKELAND, FL 33811

www.publix.com

CONSULTANT

AECOM

AECOM TECHNICAL SERVICES, INC.
800 Douglas Entrance
North Tower, 2nd Floor
Coral Gables, FL 33134
305.444.4691 tel 305.447.3580 fax
www.aecom.com

ARCHITECTURE
LICENSE NO. AA26000687

ENGINEERING
CA LIC. NO. 8115

www.aecom.com

REGISTRATION

NICHOLAS A. MYERS LICENSE LA 6667226 STATE OF FLORIDA LANDSCAPE ARCHITECT

Nicholas A Myers
Digitally signed by Nicholas A Myers
Date: 2019.08.23 09:18:43 -04'00'

NICHOLAS A. MYERS, RLA

LANDSCAPE ARCHITECT OF RECORD

THE OFFICIAL RECORD OF THIS SHEET IS THE ELECTRONIC FILE DIGITALLY SIGNED AND SEALED UNDER RULE 61G10-11.011, F.A.C.

ISSUE/REVISION

I/R	DATE	DESCRIPTION
0	AUG 23, 2019	CONSTRUCTION DOCUMENTS

PROJECT NUMBER

60601397

SHEET TITLE

IRRIGATION PLAN

SHEET NUMBER

IR-101

ARCH E1 30"x42" Approved: Checked: Designer: Project Management Initials:

Last Plotted: 8/21/2019 3:17:26 PM
Filename: S:\PROJECTS_CIVIL\PROJECTS\PUBLIX\900-DWG\5900-CAD_BIM (CIVIL)\20-SHEETS\LIR-100 IRRIGATION PLAN.DWG

Printed on ___% Post-Consumer Recycled Content Paper

©2016 AECOM Corporation