M2-1-10-HVAC OVERALL PLAN - LEVEL 1
Project Management Initials: Designer: Designer Checked: Checker Approved: ApproverARCH E1 30"x42"

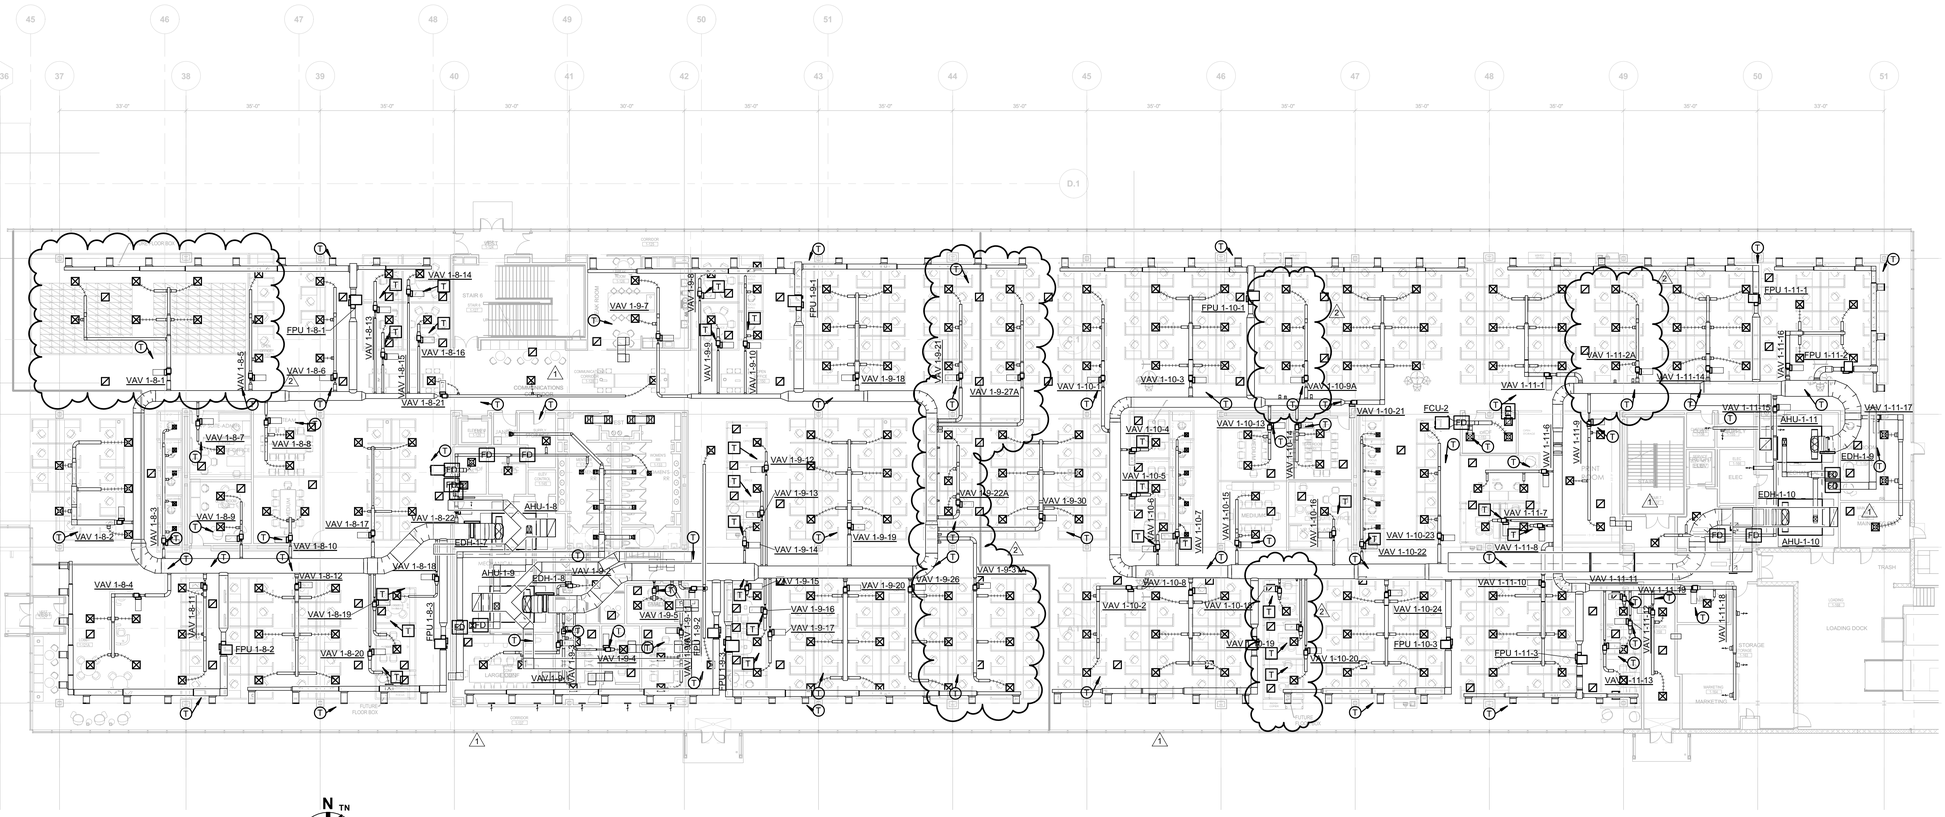

1 HVAC OVERALL PLAN - LEVEL 1
Scale: 1/16" = 1'-0"

N TN

Last Plotted: 5/12/2020 12:56:28 PM
Filename: BM 5600-0000/397-Publix HQ/60601397_Publix HQ_MECH_R2019.rvt

Printed on ___ % Post-Consumer Recycled Content Paper

©2016 AECOM Corporation

Building Inspection Division

Lakeland CITY OF LAKELAND

THESE PLANS HAVE BEEN REVIEWED FOR COMPLIANCE WITH THE CURRENT EDITION. OF THE CITY OF LAKELAND CODE OF THE CITY OF LAKELAND LAND DEVELOPMENT CODE

Date: 06/30/20

Permit Number: BLD16-00198

AECOM

BATSON-COOK CONSTRUCTION

PROJECT

PUBLIX HEADQUARTERS BUILDING ADDITION AND PARKING LOT EXPANSION

3300 PUBLIX CORPORATE PARKWAY
LAKELAND, FL 33811

CLIENT

Publix

3300 PUBLIX CORPORATE PARKWAY
LAKELAND, FL 33811

www.publix.com

CONSULTANT

AECOM

AECOM TECHNICAL SERVICES INC.
800 Douglas Entrance
North Tower, 2nd Floor
Coral Gables, FL 33134
305.444.4691 tel 305.447.3580 fax
www.aecom.com

ARCHTIECTURE
LICENSE NO. AA260000687

ENGINEERING
CA LIC. NO. 8115

www.aecom.com

REGISTRATION

JOHN TYE RECTOR
LICENSE
No. 53292
STATE OF FLORIDA
PROFESSIONAL ENGINEER

JOHN T. RECTOR, PROFESSIONAL ENGINEER, STATE OF FLORIDA, LICENSE NO. 53292
06/19/20

John T Rector
John T Rector 2020.06.19 12:46:24 -04'00'

THIS ITEM HAS BEEN DIGITALLY SIGNED AND SEALED BY JOHN T. RECTOR, PROFESSIONAL ENGINEER, STATE OF FLORIDA, LICENSE NO. 53292 ON THE DATE ADJACENT TO THE SEAL. PRINTED COPIES OF THIS DOCUMENT MUST BE VERIFIED ON ANY ELECTRONIC COPIES.

NOTICE: THE OFFICIAL RECORD OF THIS SHEET IS THE ELECTRONIC FILE SIGNED AND SEALED UNDER RULE 61G15-23.004, F.A.C.

ISSUE/REVISION

I/R	DATE	DESCRIPTION
2	MAY 01, 2020	SI-004
1	NOV. 22, 2019	SI-001
	SEP 30, 2019	100% CONSTRUCTION DOCUMENTS
	AUG 23, 2019	CONSTRUCTION DOCUMENTS
	MAY 31, 2019	35% DESIGN COMPLETION

PROJECT NUMBER

60601397

SHEET TITLE

HVAC OVERALL PLAN - LEVEL 1

SHEET NUMBER

M2-1-10