Building Inspection Division
Lakeland
THESE PLANS HAVE BEEN REVIEWED FOR COMPLIANCE WITH THE CURRENT EDITION. OF THE FLORIDA BUILDING CODE OR THE CITY OF LAKELAND LAND DEVELOPMENT CODE
Date: 06/30/20
Permit Number: BLD16-00198

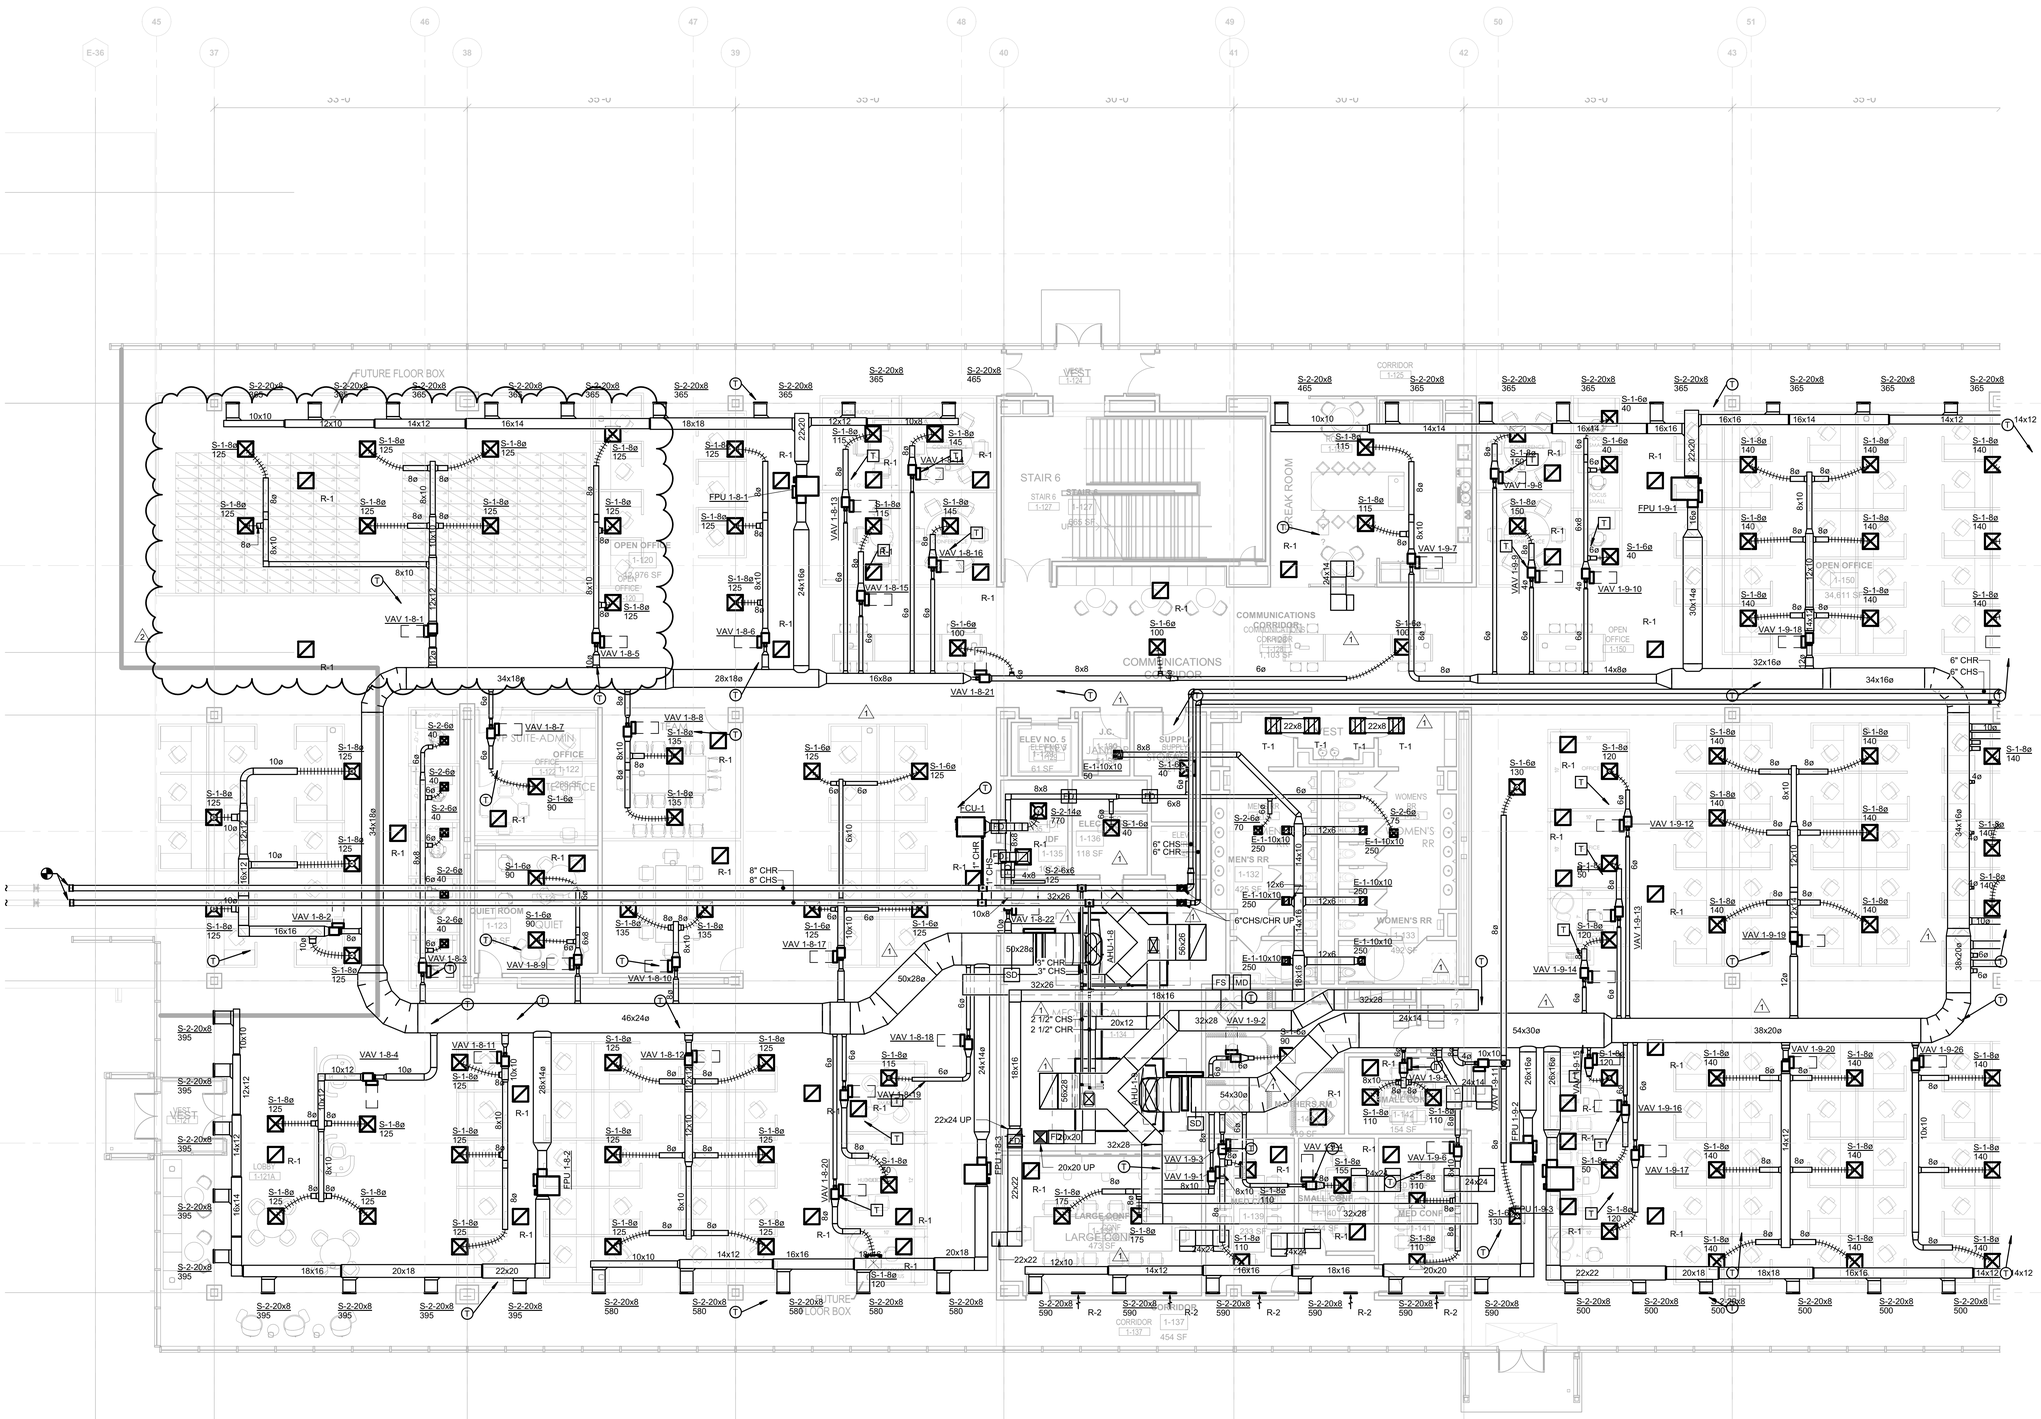


1 HVAC PARTIAL PLAN - LEVEL 1 AREA A
Scale: 1/8" = 1'-0"

N TN

# AECOM

BATSON-COOK CONSTRUCTION

## PROJECT

**PUBLIX HEADQUARTERS BUILDING ADDITION AND PARKING LOT EXPANSION**

3300 PUBLIX CORPORATE PARKWAY
LAKELAND, FL 33811

## CLIENT

Publix.

3300 PUBLIX CORPORATE PARKWAY
LAKELAND, FL 33811

www.publix.com

## CONSULTANT

**AECOM**

AECOM TECHNICAL SERVICES INC.
800 Douglas Entrance
North Tower, 2nd Floor
Coral Gables, FL 33134
305.444.4691 tel 305.447.3580 fax
www.aecom.com

ARCHITECTURE
LICENSE NO. AA260000687

ENGINEERING
CA LIC. NO. 8115

www.aecom.com

## REGISTRATION

JOHN TYE RECTOR
LICENSE
No. 53292
STATE OF FLORIDA
PROFESSIONAL ENGINEER

JOHN T. RECTOR, PROFESSIONAL ENGINEER, STATE OF FLORIDA, LICENSE NO. 53292
06/19/20

John T Rector
John T Rector
2020.06.19
12:58:32 -04'00'

THIS ITEM HAS BEEN DIGITALLY SIGNED AND SEALED BY JOHN T. RECTOR, PROFESSIONAL ENGINEER, STATE OF FLORIDA, LICENSE NO. 53292 ON THE DATE ADJACENT TO THE SEAL. PRINTED COPIES OF THIS DOCUMENT MUST BE VERIFIED ON ANY ELECTRONIC COPIES.

NOTICE: THE OFFICIAL RECORD OF THIS SHEET IS THE ELECTRONIC FILE SIGNED AND SEALED UNDER RULE 61G15-23.004, F.A.C.

## ISSUE/REVISION

| I/R | DATE | DESCRIPTION |
|---|---|---|
| 2 | MAY 01, 2020 | SI-004 |
| 1 | NOV. 22, 2019 | SI-001 |
| | SEP 30, 2019 | 100% CONSTRUCTION DOCUMENTS |
| | AUG 23, 2019 | CONSTRUCTION DOCUMENTS |
| | MAY 31, 2019 | 35% DESIGN COMPLETION |

## PROJECT NUMBER

60601397

## SHEET TITLE

**HVAC PARTIAL PLAN - LEVEL 1 AREA A**

## SHEET NUMBER

**M2-2-11**



Printed on:____% Post-Consumer Recycled Content Paper
©2016 AECOM Corporation