Building Inspection Division
THESE PLANS HAVE BEEN REVIEWED FOR COMPLIANCE WITH THE CURRENT EDITION OF THE FLORIDA BUILDING CODE
Lakeland
Date: 11/15/19
Permit Number: BLD19-06035

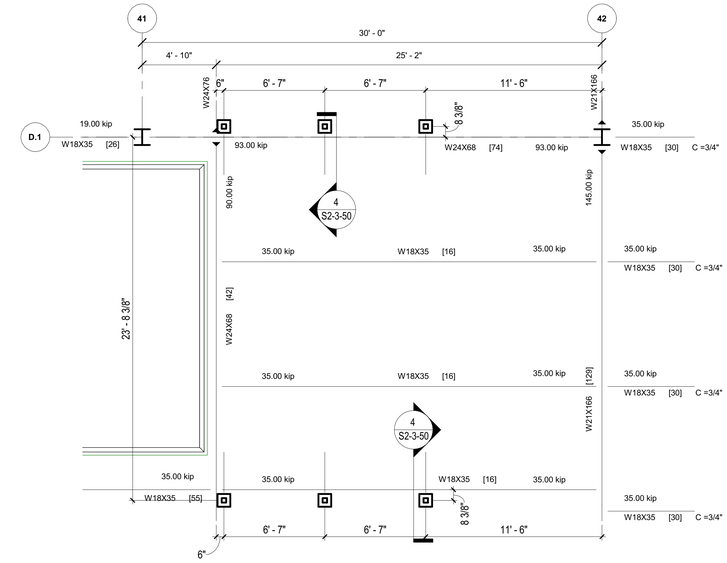

DENOTES HSS 3 1/2 x 3 1/2 x 5/16 TUBE HANGER W/ L3x3x1/4 ANGLE KICKER

REFER TO LEVEL 2 - AREA A PLAN FOR INFORMATION NOT SHOWN HERE

1 ENLARGED LEVEL 2 - AREA A

S2-3-50 | REF: S2-3-50 SCALE: 1/4" = 1'-0"

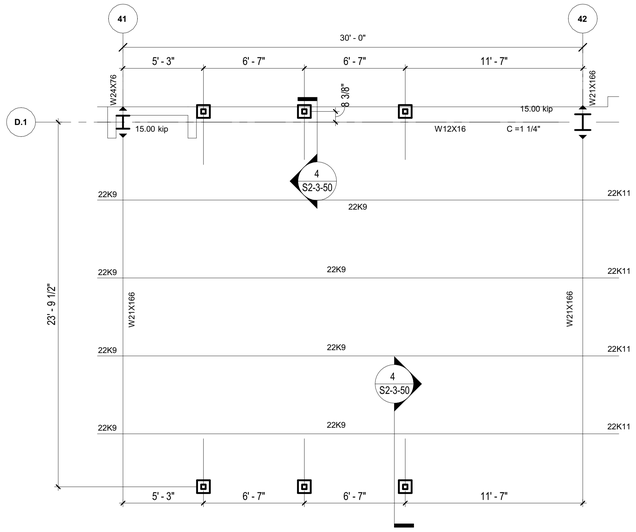

DENOTES HSS 3 1/2 x 3 1/2 x 5/16 TUBE HANGER W/ L3x3x1/4 ANGLE KICKER

REFER TO ROOF - AREA A PLAN FOR INFORMATION NOT SHOWN HERE

3 ENLARGED ROOF - AREA A

S2-3-50 | SCALE: 1/4" = 1'-0"

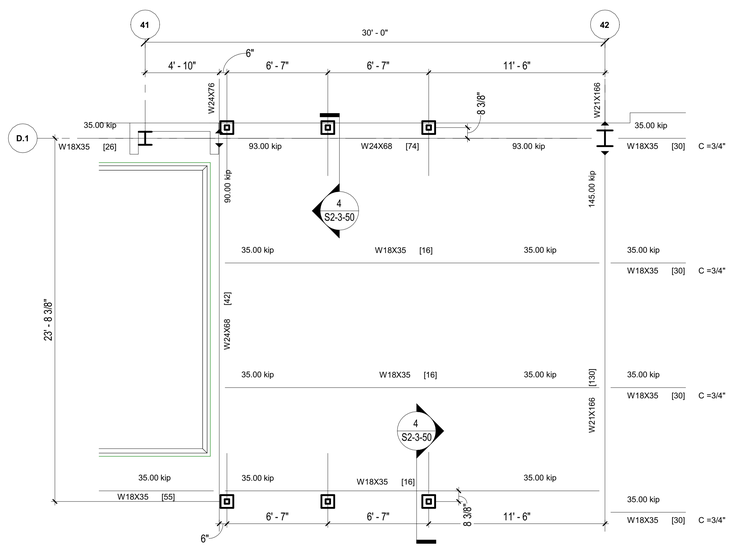

DENOTES HSS 3 1/2 x 3 1/2 x 5/16 TUBE HANGER W/ L3x3x1/4 ANGLE KICKER

REFER TO LEVEL 3 - AREA A PLAN FOR INFORMATION NOT SHOWN HERE

2 ENLARGED LEVEL 3 - AREA A

S2-3-50 | REF: S2-3-50 SCALE: 1/4" = 1'-0"

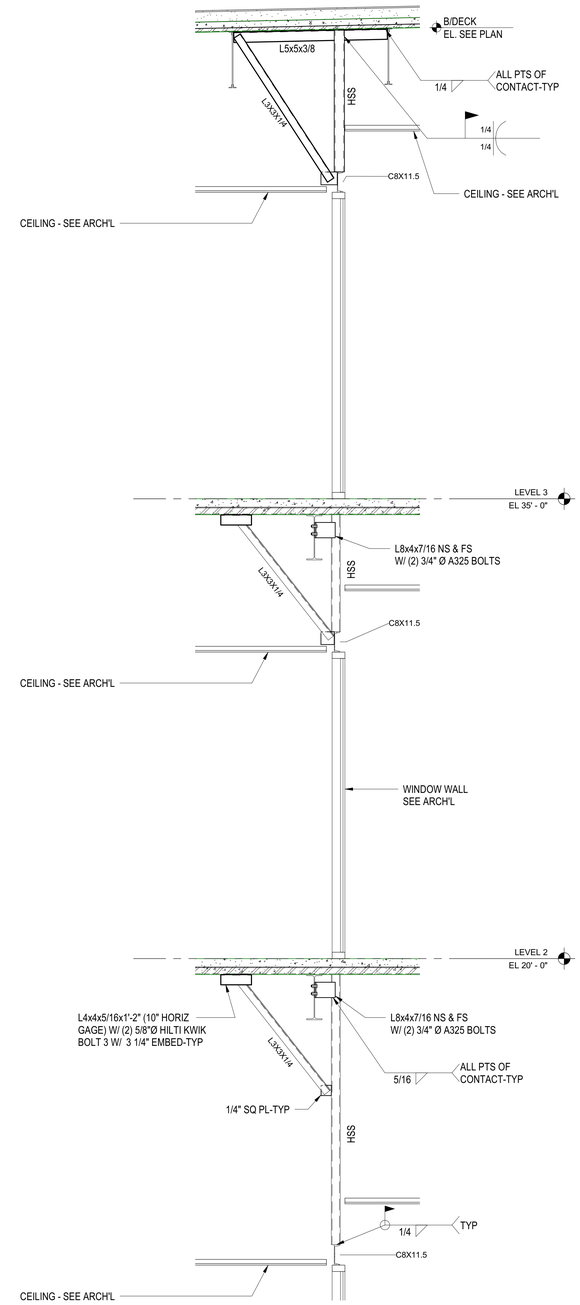

NOTE:
DETAILS TO BE USED AT ALL INTERIOR WINDOW WALL LOCATIONS

4 SECTION

S2-3-50 | REF: S2-3-50 SCALE: 1/2" = 1'-0"

SCALE: 1/2" = 1'-0" 0 1' 2' 4' 6'

SCALE: 1/4" = 1'-0" 0 1' 2' 4' 8' 12'

AECOM
BATSON-COOK CONSTRUCTION

PROJECT

PUBLIX HEADQUARTERS BUILDING ADDITION AND PARKING LOT EXPANSION

3300 PUBLIX CORPORATE PARKWAY
LAKELAND, FL 33811

CLIENT

Publix

3300 PUBLIX CORPORATE PARKWAY
LAKELAND, FL 33811

www.publix.com

CONSULTANT

AECOM

AECOM TECHNICAL SERVICES, INC.
800 Douglas Entrance
North Tower, 2nd Floor
Coral Gables, FL 33134
305.444.4691 tel 305.447.3580 fax
www.aecom.com

ARCHITECTURE
LICENSE NO. AA26000687

ENGINEERING
CA LIC. NO. 8115

http://www.aecom.com

REGISTRATION

VINCENT RAJ VACCARELLO-WADEHRA, PROFESSIONAL ENGINEER, STATE OF FLORIDA, LICENSE NO. 81224

THIS ITEM HAS BEEN DIGITALLY SIGNED AND SEALED BY VINCENT RAJ VACCARELLO-WADEHRA, PROFESSIONAL ENGINEER, STATE OF FLORIDA, LICENSE NO. 81224 ON THE DATE INDICATED HERE. PRINTED COPIES OF THIS DOCUMENT ARE NOT CONSIDERED SIGNED AND SEALED AND THE SIGNATURE MUST BE VERIFIED ON ANY ELECTRONIC COPIES.

Vincent R Vaccarello -Wadehra
Digitally signed by Vincent R Vaccarello-Wadehra
Date: 2019.08.22 18:00:52 -04'00'

ISSUE/REVISION

I/R	DATE	DESCRIPTION
0	AUGUST 23, 2019	CONSTRUCTION DOCUMENTS
	AUGUST 16, 2019	90% CONSTRUCTION DOCUMENTS

PROJECT NUMBER

60601397

SHEET TITLE

ENLARGED PLANS

SHEET NUMBER

S2-3-50

This drawing has been prepared for the use of AECOM's client and may not be used, reproduced or relied upon by third parties, except as agreed by AECOM and its client, as required by law or for use by governmental reviewing agencies. AECOM accepts no responsibility, and denies any liability whatsoever to any party that modifies this drawing without AECOM's express written consent. Do not scale this document. All measurements must be obtained from the stated dimensions.

NOTICE: THE OFFICIAL RECORD OF THIS SHEET IS THE ELECTRONIC FILE SIGNED AND SEALED UNDER RULE 61G15-23.004, F.A.C.

©2016 AECOM Corporation

Project Management Initials: Designer: Designer Checked: Checker Approved: Approver/RCH E1 30"x42"
Last Plotted: 8/22/2019 5:38:23 PM
Filename: BM 300:/60601397-Publix HQ/60601397_Publix HQ_STRUCT_R2019.rvt

Printed on ___% Post-Consumer Recycled Content Paper