EXISTING CONDITIONS TOPOGRAPHIC SURVEY
Designer: NJR Checked: KMW Approved: DWS ARCH E1 30"x42"
Project Management Initials:

Building Inspection Division
THESE PLANS HAVE BEEN REVIEWED FOR COMPLIANCE WITH THE CURRENT EDITION OF THE FLORIDA BUILDING CODE
Lakeland Building & Inspections
Date: 11/15/19
Permit Number: BLD19-06035

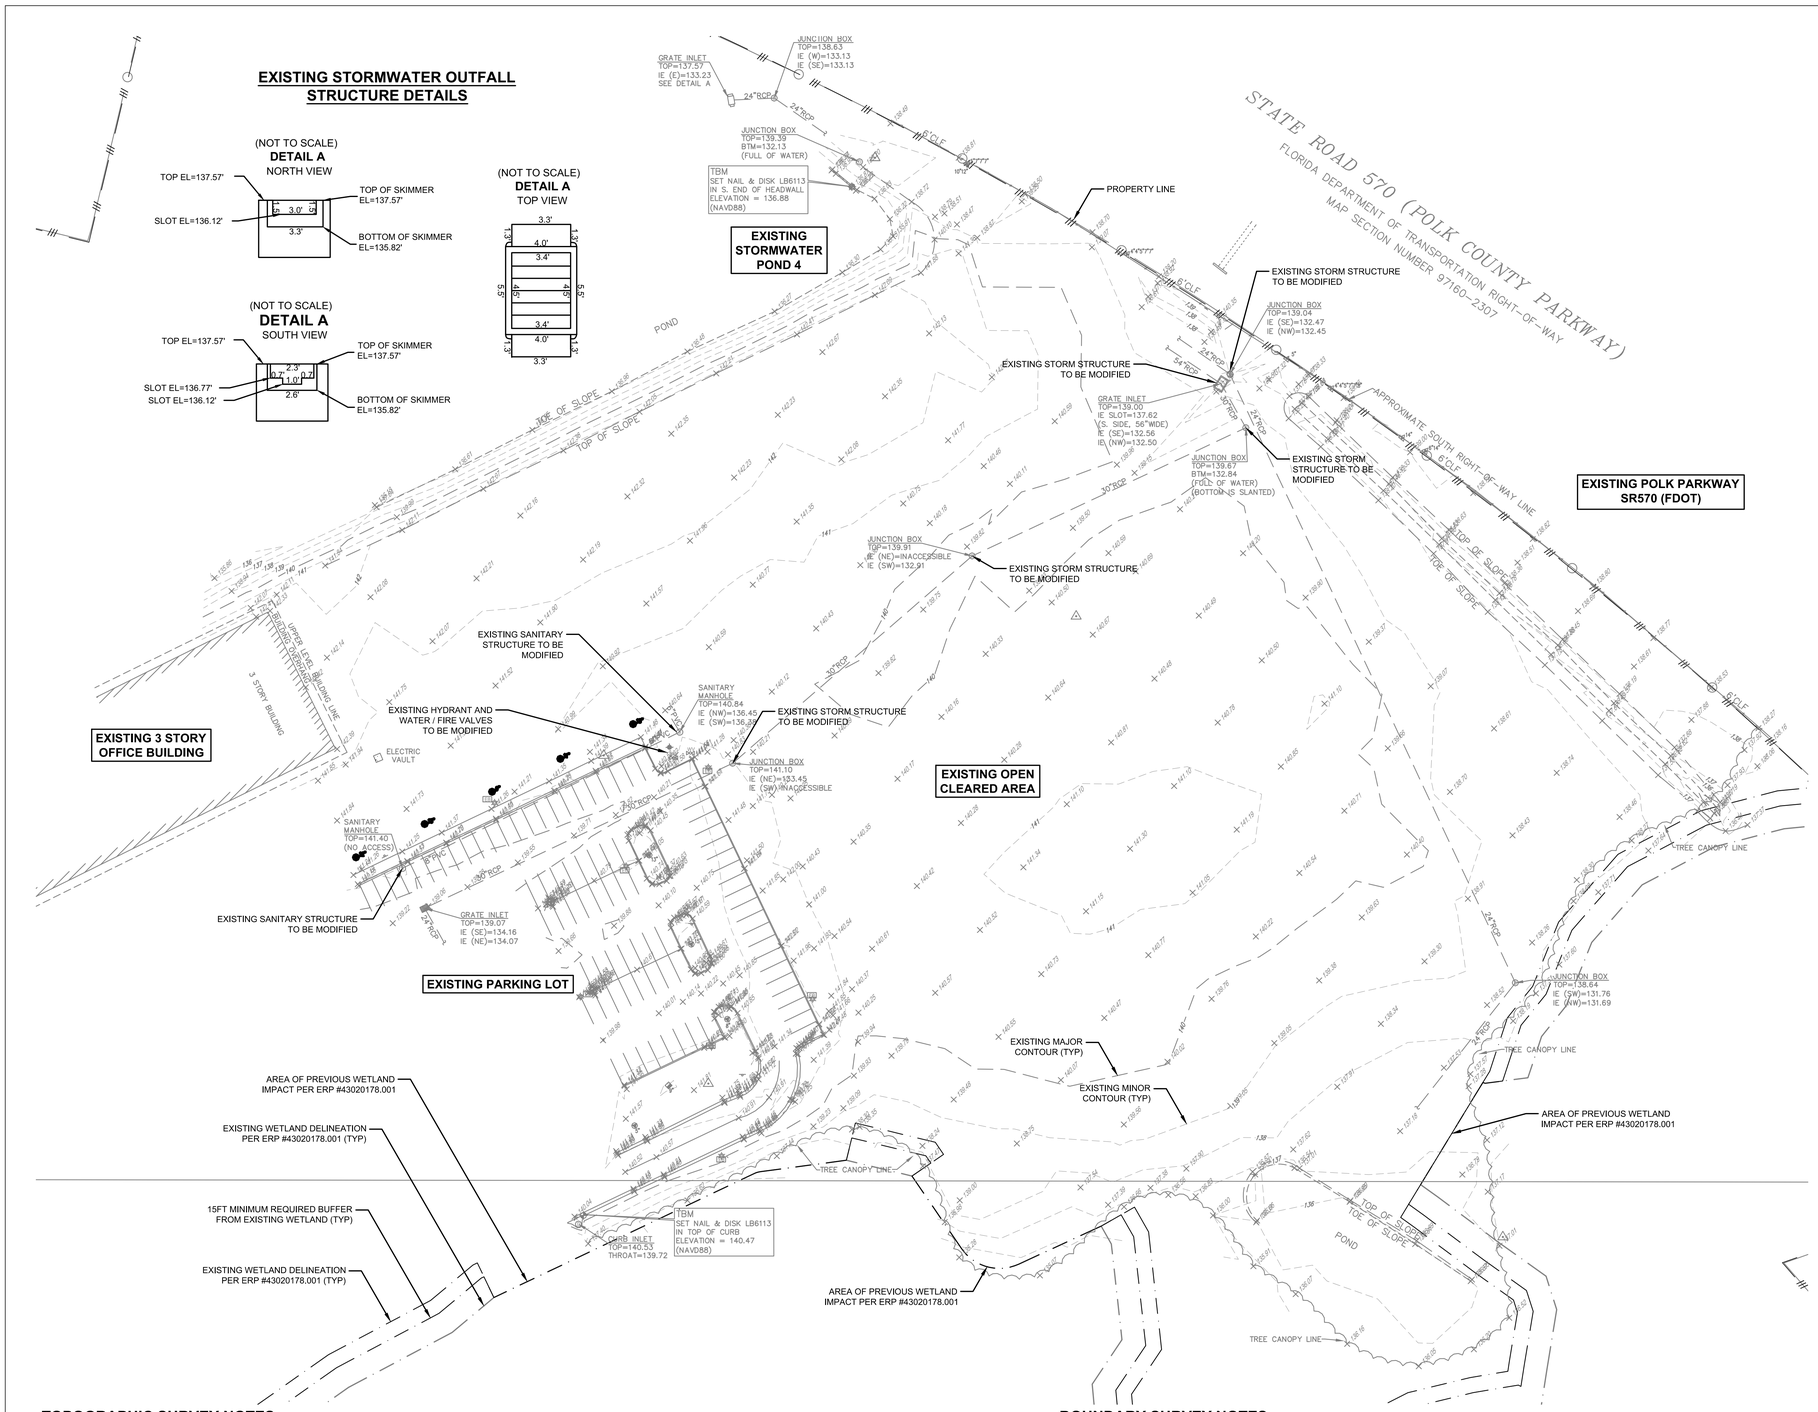

KEY MAP

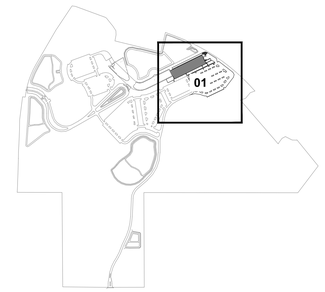

A/C = AIR CONDITIONER UNIT
BLDG = BUILDING
(C) = CALCULATED DATA
CCR = CERTIFIED CORNER RECORD
CLF = CHAIN LINK FENCE
CMP = CORRUGATED METAL PIPE
CONC = CONCRETE
COR = CORNER
CPB = CONDOMINIUM PLAT BOOK
CT = CURB TIE
(D) = DEED DATA
DB = DEED BOOK
DIP = DUCTILE IRON PIPE

ECMP = ELLIPTICAL CORRUGATED METAL PIPE
EL = ELEVATION
EP = EDGE OF PAVEMENT
ERCP = ELLIPTICAL REINFORCE CONCRETE PIPE
(F) = FIELD DATA
FCM = FOUND CONCRETE MONUMENT
FDOT = FLORIDA DEPARTMENT OF TRANSPORTATION
FIR = FOUND IRON ROD
FND = FOUND NAIL & DISC
FOP = FOUND OPEN PIPE
FPP = FOUND PINCHED PIPE
FRRS = FOUND RAILROAD SPIKE
F/T = FENCE TIE

FXC = FOUND X-CUT
GE = GRATE ELEVATION
IE = INVERT ELEVATION
(L) = LEGAL DESCRIPTION DATA
LB = LICENSED BUSINESS
LS = LICENSED SURVEYOR
MAS = MASONRY
MHW = MEAN HIGH WATER
NP = NORMAL POOL
O/A = OVERALL
OR = OFFICIAL RECORDS BOOK
(P) = PLAT DATA
PB = PLAT BOOK

PG = PAGE
PLS = PROFESSIONAL LAND SURVEYOR
POB = POINT OF BEGINNING
POC = POINT OF COMMENCEMENT
PRM = PERMANENT REFERENCE MONUMENT
PSM = PROFESSIONAL SURVEYOR & MAPPER
P/T = PAVEMENT TIE
PVC = POLY VINYL CHLORIDE
RCP = REINFORCE CONCRETE PIPE
RLS = REGISTERED LAND SURVEYOR
R/W = RIGHT-OF-WAY
SEC = SECTION
SHW = SEASONAL HIGH WATER

SIR = SET IRON ROD 1/2" LB 6113
SND = SET NAIL & DISC LB 6113
SR = STATE ROAD
S/T = SIDEWALK TIE
STY = STORY
SW = SIDEWALK
TBM = TEMPORARY BENCH MARK
(TYP) = TYPICAL
VCP = VITRIFIED CLAY PIPE
W/ = WITH
WF = WOOD FENCE
W/T = WALL TIE

= TOP OF BANK
= TOE OF SLOPE or CENTER LINE OF DITCH
= 6' CHAIN LINK FENCE UNLESS OTHERWISE NOTED
= OVERHEAD UTILITY LINES
= APPROXIMATE LOCATION OF UNDERGROUND GAS LINE
= APPROXIMATE LOCATION OF UNDERGROUND WATER LINE
= APPROXIMATE LOCATION OF UNDERGROUND FORCEMAIN
= APPROXIMATE LOCATION OF UNDERGROUND RECLAIMED WATER LINE
= APPROXIMATE LOCATION OF UNDERGROUND SANITARY SEWER LINE
= APPROXIMATE LOCATION OF UNDERGROUND STORM SEWER LINE

+25.25 = POINT OF ELEVATION
25.2' = DIMENSION FROM BUILDING TO BOUNDARY / RIGHT-OF-WAY LINE
= BACKFLOW PREVENTER
= BOLLARD or POST
= BOX, CABLE TELEVISION
= BOX, ELECTRIC UTILITY
= BOX, ELECTRIC UTILITY (TRANSFORMER)
= BOX, TELEPHONE
= DECORATIVE LIGHT POLE
= ELECTRIC OUTLET
= FIRE HYDRANT
= FLAGPOLE
= FLARED END SECTION
= GRATE INLET
= GROUND LIGHT
= GUY ANCHOR
= LIGHT POLE, CONCRETE
= LIGHT POLE, METAL
= LIGHT POLE, WOOD
= MAILBOX
= MANHOLE, ELECTRIC
= MANHOLE, GREASE TRAP
= MANHOLE, SANITARY SEWER
= STORM SEWER STRUCTURE
= MANHOLE, TELEPHONE
= METER, ELECTRIC
= METER, GAS
= METER, RECLAIMED WATER
= METER, WATER
= MITERED END SECTION
= MONITORING WELL
= PEDESTRIAN CROSSING SIGNAL
= SANITARY CLEANOUT
= SCHEDULE B-2 ITEM
= TELEPHONE RISER
= TRAFFIC SIGN
= TRAFFIC SIGNAL BOX
= TRAFFIC SIGNAL POLE
= UNDERGROUND CABLE TELEVISION MARKER
= UNDERGROUND CABLE TELEVISION WARNING SIGN
= UNDERGROUND ELECTRIC MARKER
= UNDERGROUND ELECTRIC WARNING SIGN
= UNDERGROUND FIBER OPTIC MARKER
= UNDERGROUND FIBER OPTIC WARNING SIGN
= UNDERGROUND FORCEMAIN MARKER
= UNDERGROUND FORCEMAIN WARNING SIGN
= UNDERGROUND GAS MARKER
= UNDERGROUND GAS WARNING SIGN
= UNDERGROUND RECLAIMED WATER MARKER
= UNDERGROUND RECLAIMED WATER WARNING SIGN
= UNDERGROUND SANITARY SEWER MARKER
= UNDERGROUND SANITARY SEWER WARNING SIGN
= UNDERGROUND TELEPHONE MARKER
= UNDERGROUND TELEPHONE WARNING SIGN
= UNDERGROUND WATER MARKER
= UNDERGROUND WATER WARNING SIGN
= UTILITY POLE, CONCRETE
= UTILITY POLE, METAL
= UTILITY POLE, WOOD
= VALVE, GAS
= VALVE, RECLAIMED WATER
= VALVE, SANITARY
= VALVE, WATER
= WELL

STORM CURB INLETS

= CONCRETE
= ASPHALT
= CONCRETE PAVERS
= BRICK
52.15 = BACK OF CURB
51.61 = FLOWLINE
51.63 = EDGE OF PAVEMENT
EXISTING MAJOR CONTOUR
EXISTING MINOR CONTOUR
EXISTING SPOT ELEVATION

= BAY TREE
= BOTTLE BRUSH TREE
= CAMPHOR TREE
= CEDAR
= CHINABERRY TREE
= CITRUS TREE
= CYPRESS TREE
= ELM TREE
= EUCALYPTUS TREE
= MAGNOLIA TREE
= MAPLE TREE
= MULBERRY TREE
= OAK TREE
= OTHER SPECIES
= PALM TREE
= PECAN TREE
= PERSIMMON TREE
= PINE TREE
= SYCAMORE TREE
= WAX MYRTLE TREE
= WILLOW TREE

NORTH
0 40' 80'
GRAPHIC SCALE

TOPOGRAPHIC SURVEY NOTES

1. THE PURPOSE OF THIS SURVEY IS TO LOCATE THE GROUND TOPOGRAPHY IN A SPECIFIED AREA FOR FUTURE DESIGN AND CONSTRUCTION.
2. SURVEY MAP AND REPORT OR THE COPIES THEREOF ARE NOT VALID WITHOUT THE SIGNATURE AND THE ORIGINAL RAISED SEAL OF A FLORIDA LICENSED SURVEYOR AND MAPPER. ADDITIONS OR DELETIONS TO SURVEY MAPS OR REPORTS BY OTHER THAN THE SIGNING PARTY OR PARTIES IS PROHIBITED.
3. NO EXCAVATION WAS PERFORMED TO VERIFY THE LOCATION OR EXISTENCE OF ANY UNDERGROUND UTILITIES, ENCROACHMENTS, IMPROVEMENTS, STRUCTURES OR FOUNDATIONS. UNDERGROUND UTILITY LINE LOCATIONS (IF SHOWN HEREON) ARE BASED UPON UTILITY PROVIDER ATLASES AND VISIBLE SURFACE EVIDENCE.
4. RE-USE OF THIS SURVEY FOR PURPOSES OTHER THAN WHICH IT WAS INTENDED, WITHOUT WRITTEN VERIFICATION, WILL BE AT THE RE-USERS SOLE RISK AND WITHOUT LIABILITY TO THE SURVEYOR. NOTHING HEREIN SHALL BE CONSTRUED TO GIVE ANY RIGHTS OR BENEFITS TO ANYONE OTHER THAN THOSE TO WHOM CERTIFIED.
5. ALL FOUND POINTS ARE UNMARKED UNLESS OTHERWISE NOTED. ALL PERIMETER BEARINGS AND DISTANCES ARE ALSO FIELD MEASURED UNLESS NOTED.
6. THIS SURVEY IS NOT INTENDED TO SHOW THE LOCATION OR EXISTENCE OF ANY JURISDICTIONAL, HAZARDOUS OR ENVIRONMENTALLY SENSITIVE AREAS.
7. ANY ZONING INFORMATION SHOWN OR NOTED HEREON IS BASED ON INFORMATION AVAILABLE DURING THE PREPARATION OF THE SURVEY. THIS INFORMATION SHOULD BE VERIFIED WITH THE GOVERNING AUTHORITY PRIOR TO ANY DETERMINATIONS OR DESIGN.
8. a
8. SHOWN ANYWHERE ON THIS SURVEY, THE WORD "CERTIFY" IS UNDERSTOOD TO BE AN EXPRESSION OF A PROFESSIONAL OPINION BASED UPON THE SURVEYOR'S BEST KNOWLEDGE, INFORMATION AND BELIEF, AND THAT IT THUS CONSTITUTES NEITHER A GUARANTEE NOR A WARRANTY.
9. UNLESS OTHERWISE INDICATED, THE PROPERTY DESCRIPTION AND EASEMENTS SHOWN WERE FURNISHED TO POLARIS ASSOCIATES, INC. AND ARE PRESUMED TO BE CORRECT. NO SEARCH OF ANY PUBLIC RECORDS, FOR EASEMENTS, DEEDS, ETC., WAS PERFORMED BY THIS FIRM FOR THE COMPLETION OF THIS SURVEY AND THERE MAY BE ADDITIONAL RESTRICTIONS THAT MAY BE FOUND IN THE PUBLIC RECORDS OF THIS COUNTY.
10. THIS SURVEY WAS PREPARED WITHOUT THE BENEFIT OF AN ABSTRACT OF TITLE AND MAY BE SUBJECT TO EASEMENTS, RESTRICTIONS, RIGHTS-OF-WAY AND OTHER MATTERS OF RECORD.
11. ELEVATIONS ARE BASED ON NATIONAL GEODETIC SURVEY MONUMENT "J 742" HAVING AN ELEVATION OF 139.14 NORTH AMERICAN VERTICAL DATUM 1988 (NAVD 88). TO OBTAIN NATIONAL GEODETIC VERTICAL DATUM 1929 (NGVD 29) ELEVATIONS, ADD 0.85 FEET TO THE ELEVATIONS SHOWN HEREON.
12. TREES 4" IN DIAMETER AND LARGER HAVE BEEN LOCATED WITH COMMON NAME AND APPROXIMATE DIAMETER BREAST HIGH. SMALLER TREES, NON-PROTECTED SPECIES (INCLUDING ORNAMENTALS) AND TREES WITHIN JURISDICTIONAL AREAS (IF ANY) HAVE NOT BEEN LOCATED. TREES BY NATURE ARE IRREGULAR IN SIZE AND SHAPE. EVERY EFFORT IS MADE TO ACCURATELY LOCATE TREES. THE TREE LOCATION IS THE CENTER OF THE TREE. THIS LOCATION MAY BE DIFFERENT IF LOCATED FROM A DIFFERENT DIRECTION. ALL TREE LOCATIONS SHOULD BE FIELD CHECKED IF CRITICAL TO DESIGN.
13. THIS SURVEY IS BASED ON U.S. FEET.

BOUNDARY SURVEY NOTES

UNDERGROUND IMPROVEMENTS, IF ANY, HAVE NOT BEEN LOCATED. SEE SHEET TWO OF TWO FOR WETLAND LOCATION. THIS SURVEY WAS PERFORMED WITHOUT THE BENEFIT OF AN ABSTRACT OR TITLE OPINION, THEREFORE EASEMENTS OR OTHER ENCUMBRANCES MAY EXIST THAT ARE NOT SHOWN HEREON. BEARINGS BASED ON THE SOUTH LINE OF STATE ROAD NUMBER 570 (POLK COUNTY PARKWAY) AS SHOWN ON FLORIDA DEPARTMENT OF TRANSPORTATION RIGHT-OF-WAY MAP SECTION NUMBER 97160-2307, BEING NORTH 69°51'05" EAST. THE PROPERTY SHOWN HEREIN LIES IN ZONES "A" AND "C" AS SHOWN ON THE FLOOD INSURANCE RATE MAP PER COMMUNITY PANEL NUMBERS 120261 0295 B AND 120261 0475 D AS PREPARED BY THE FEDERAL EMERGENCY MANAGEMENT AGENCY. EFFECTIVE DATES JANUARY 19, 1983 AND OCTOBER 18, 1988. THE ABOVE STATEMENT IS FOR INFORMATION ONLY AND THIS SURVEYOR ASSUMES NO LIABILITY FOR THE CORRECTNESS OF THE CITED MAP. IN ADDITION, THE ABOVE STATEMENT DOES NOT REPRESENT THIS SURVEYOR'S OPINION OF THE PROBABILITY OF FLOODING. DUE TO THE SIZE AND TERRAIN OF THE SUBJECT PARCEL, INTERIOR FENCES AND OTHER POSSIBLE IMPROVEMENTS HAVE NOT BEEN LOCATED. MAINTAINED RIGHT-OF-WAY AS PER MAP BOOK 1. PAGE 60-65, DATED FEBRUARY 7, 1968, DOES NOT REPRESENT THE RIGHT-OF-WAY AS INDICATED IN THE FIELD ON THE DATE OF SURVEY. THE APPARENT MAINTAINED RIGHT-OF-WAY WAS MONUMENTED. HEADWALLS AND CULVERTS ALONG STATE ROAD 570 APPEARS TO BE CONSTRUCTED FOR THE PURPOSE OF MAINTAINING NATURAL WATER FLOW.

TOPOGRAPHIC SURVEY PROVIDED BY:
POLARIS ASSOCIATES, INC.
BY DAN H. RIZZUTO (LS#5227),
DATED JUNE 27, 2019.

BOUNDARY SURVEY PROVIDED BY:
CHASTAIN SKILLMAN,
DATED DECEMBER 8, 1999.

AECOM
BATSON-COOK CONSTRUCTION

PROJECT

PUBLIX HEADQUARTERS BUILDING ADDITION AND PARKING LOT EXPANSION

3300 PUBLIX CORPORATE PARKWAY
LAKELAND, FL 33811

CLIENT

Publix
3300 PUBLIX CORPORATE PARKWAY
LAKELAND, FL 33811

www.publix.com

CONSULTANT

AECOM

AECOM TECHNICAL SERVICES, INC.
800 Douglas Entrance
North Tower, 2nd Floor
Coral Gables, FL 33134
305.444.4691 tel 305.447.3580 fax
www.aecom.com

ARCHITECTURE
LICENSE NO. AA26000687

ENGINEERING
CA LIC. NO. 8115

www.aecom.com

Digitally signed by Dennis W Syrja
Date: 2019.08.23 10:44:04 -04'00'

REGISTRATION

DENNIS W. SYRJA
LICENSE No. 43423
STATE OF FLORIDA
PROFESSIONAL ENGINEER

DENNIS W. SYRJA, PE
ENGINEER OF RECORD

NOTICE: THE OFFICIAL RECORD OF THIS SHEET IS THE ELECTRONIC FILE SIGNED AND SEALED UNDER RULE 61G15-23.004, F.A.C.

THIS ITEM HAS BEEN DIGITALLY SIGNED AND SEALED BY DENNIS W. SYRJA, P.E. ON THE DATE ADJACENT TO THE SEAL.

PRINTED COPIES OF THIS DOCUMENT ARE NOT CONSIDERED SIGNED AND SEALED AND THE SIGNATURE MUST BE VERIFIED ON ANY ELECTRONIC COPIES.

ISSUE/REVISION

I/R	DATE	DESCRIPTION
0	AUG 23, 2019	CONSTRUCTION DOCUMENTS

PROJECT NUMBER

60601397

SHEET TITLE

EXISTING CONDITIONS TOPOGRAPHIC SURVEY

SHEET NUMBER

V-101

Last Posted: 8/22/2019 8:20:44 PM
Filename: S:\PROJECTS_CIVIL\PROJECTS\PUBLIX\900-CWDS\900-CAD_BIM (CIVIL)\20-SHEETS\CIV-101 EXISTING COND TOPO SURVEY.DWG

Printed on ___% Post-Consumer Recycled Content Paper

©2016 AECOM Corporation